
PROYECTO COCINA MODULAR ARQUIFY


PLANTA GENERAL Y ELEVACIONES (3 MÓDULOS)

VISTA PLANTA GENERAL (ARQUITECTURA)

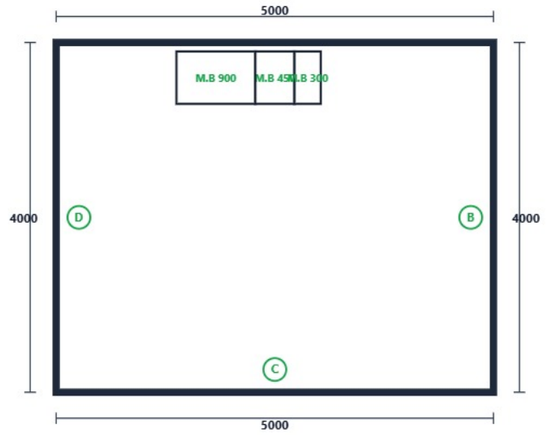

A VISTA FRONTAL A

L = 5000 mm

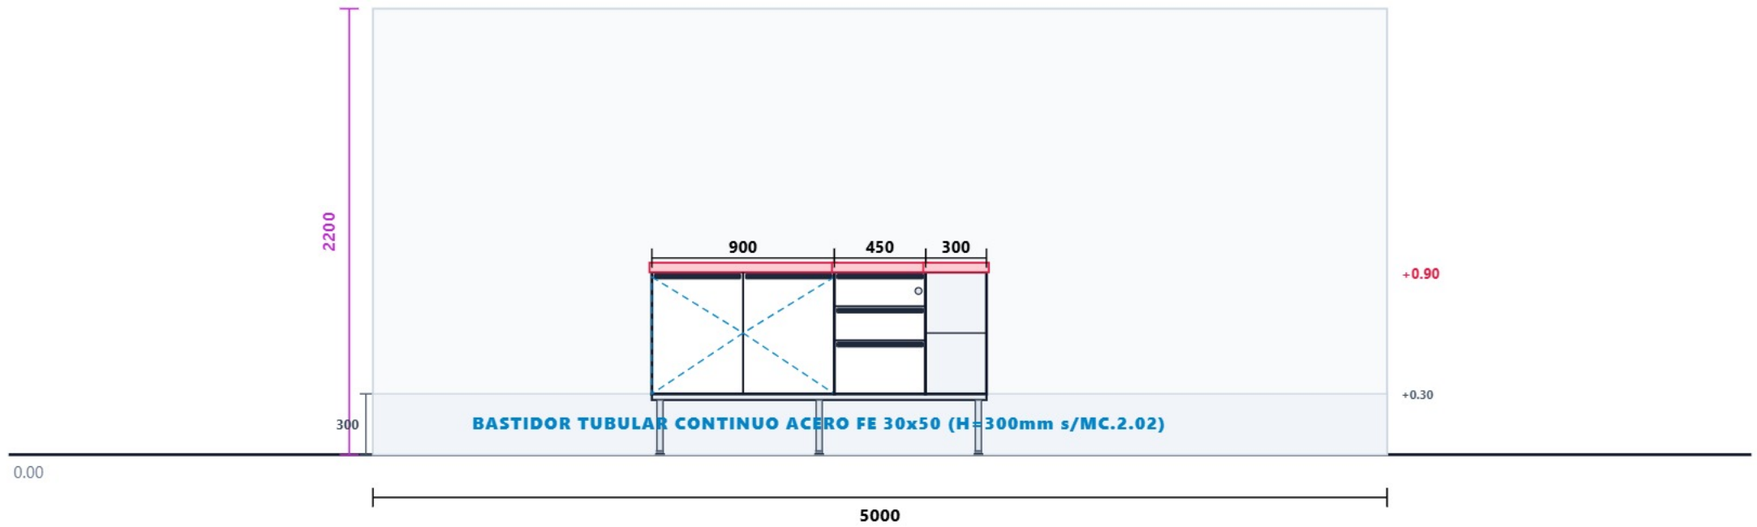

Zócalo H=300 mm | Murales con puertas y anclajes

Costados / Casco: Abet Laminati / Provelcar Blanco Interni

PROYECTO COCINA ARQUIFY

CLIENTE: CLIENTE PARTICULAR
LÁMINA: PROYECTO COCINA MODULAR ARQUIFY
CONTENIDO: PLANTA GENERAL Y ELEVACIONES

DIBUJANTE: ARQUIFY BIM CAD FECHA: 24/10/2026

ESPECIFICACIONES CLÍNICAS & ARQUITECTURA

- **NORMATIVA:** Ficha Técnica MC.2.02 SACYR • Mobiliario Clínico
- **BASTIDOR SANITARIO:** Tubular FE 30x50x1.5mm h=300 mm libres del suelo
- **NIVEL CUBIERTA:** N.P.T. +0.90 m | Krion Solid Surface 12mm

Normativa: **ISO 128 / NCh Arquitectura**

SIMBOLOGÍA DE PLANTA

- MURO / VISTA
- COTA TOTAL
- PROYECCIÓN AÉREOS
- COTA ALTURA
- NIVEL P.T.

IDENT. ETIQ. PL-01

LÁMINA: 01 / 17
ESCALA: 1:50 (A3)

arquify


LÁMINA DE FABRICACIÓN: BASTIDOR TUBULAR METÁLICO CONTINUO

Estructura autoportante unificada en FE 30×50×1.5mm (BLANCO EPÓXICO) + patines reguladores sanitarios M10 a 300mm del suelo.

ACABADO / MATERIAL: BLANCO EPÓXICO

CÓDIGO DE ELEMENTO: MC.2.02-EST

BANCADA BASTIDOR CONTINUO #1: L = 1650 MM × P = 626 MM × H = 300 MM

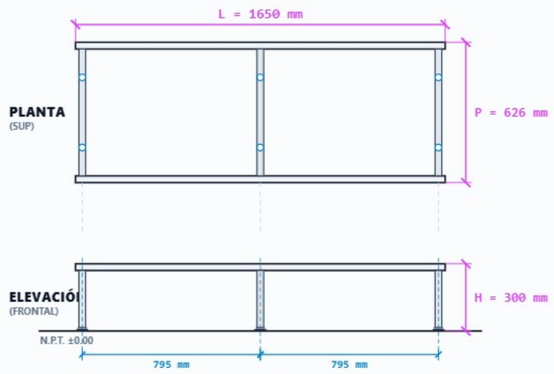



DESPIECE DE CORTES Y MATERIALES (HERRERÍA CLÍNICA / SACYR)

Total lineal acero: **6.41 m** • Barras 6m: **2 un**

Pieza / Perfil	Sección / Material	Cant. Unit.	Largo Unit.	Total Lineal	Corte / Acabado / Especificación
Larguero Longitudinal Frontal y Trasero	FE 30×50×1.5mm	**2**	1650 mm	3.30 m	Corte a 90° escuadra. Tubo continuo sin empalmes. Tratamiento fosfatizado + Pintura electrostática epóxica al horno Blanco Puro RAL 9010.
Travesaños Transversales de Amarre	FE 30×50×1.5mm	**3**	526 mm	1.58 m	Soldadura continua pulida a ras. Perforación Ø6mm para fijación.
Fustes Verticales de Pata Tubular	FE 30×50×1.5mm	**6**	256 mm	1.54 m	Base sellada con pletina electrosoldada y tuerca embutida M10.
Patín Regulador Sanitario Nivelador	Rosca M10 × 40mm	**6**	H=14 (+15) mm	–	Vástago de acero M10 con base cilíndrica de goma antideslizante lavable.

NOTAS DE TALLER: 1. Soldadura continua bajo atmósfera controlada sin porosidad. 2. Todas las aristas y cordones exteriores deben quedar enrasados y desbastados con disco abrasivo grano 120/240. 3. Terminación: Pintura electrostática en polvo termoendurecible horneada a 200°C, color Blanco Epóxico Sanitario RAL 9010. **DESPEJE SANITARIO: 300 mm N.P.T.**


NV-CAB_1 - COCINA MODULAR

MUEBLE BASE B-1 (TOTAL: 450 X 900 X 600 MM | CASCO: 450 X 600 X 570 MM)

Estructura: Abet Laminati / Provelcar Blanco Interni (HPL 0.9mm + Sustrato MDF 18mm -> Espesor final 20mm) **Frentes:** Abet Laminati / Provelcar Blanco Interni (HPL 0.9mm + Sustrato MDF 18mm -> Espesor final 20mm)


Trasera: Abet Laminati / Provelcar Blanco Interni (HPL 0.9mm + Sustrato MDF 18mm -> Espesor final 20mm)

VISTA DE PLANTA

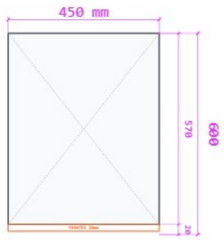


VISTA FRONTAL

VISTA LATERAL

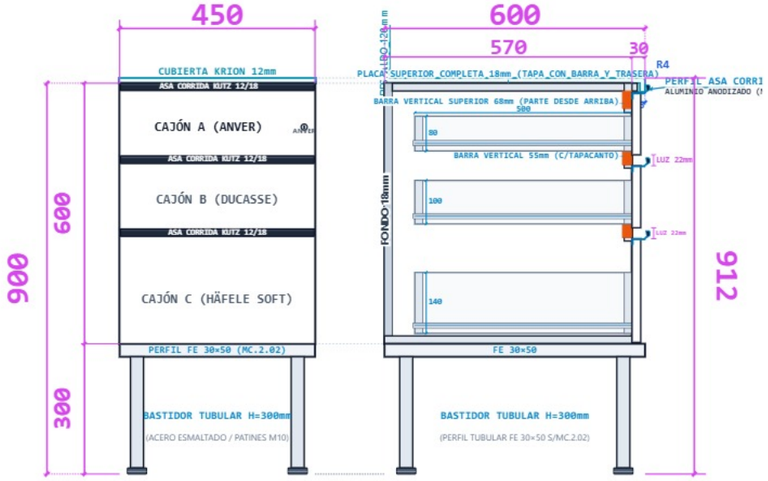

LATERAL

2 UN 18mm

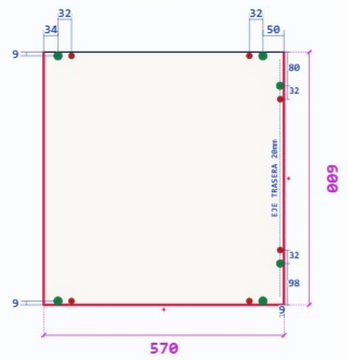


Laterales del gabinete

DXF CNC

PISO

1 UN 18mm

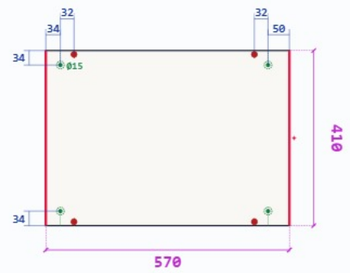


Piso del gabinete con sellado higiénico frontal y posterior (Bastidor metálico MC.2.02)

DXF CNC

TAPA SUPERIOR COMPLETA

1 UN 18mm

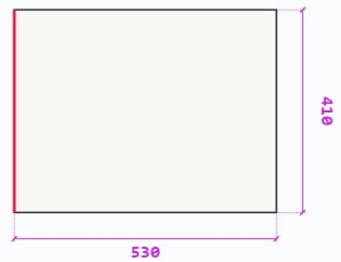


Placa superior completa de melamina que topa con la trasera y con la barra frontal superior

DXF CNC

BARRA FRONTAL SUPERIOR

1 UN 18mm

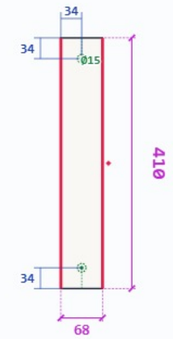


Barra frontal superior vertical bajo tapa (Alto 68mm con tapacanto incluido)

DXF CNC

BARRAS FRONTALES INTERMEDIAS

2 UN 18mm

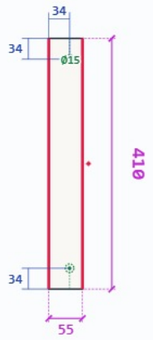


Barras frontales verticales de amarre y separación entre cajones (Alto 55mm con tapacanto incluido)

DXF CNC

FONDO TRASERA (MDF 18MM HPL)

1 UN 20mm

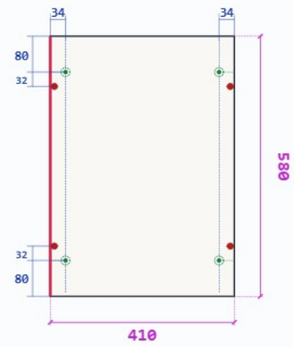


Tapa trasera de melamina/HPL 20mm que parte desde la cara superior del piso hasta la cota superior

DXF CNC

FRENTE CAJÓN 3 INFINERIOR (C)

1 UN 20mm (HPL s/ MDF 18mm)

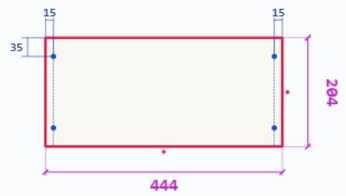

Frente HPL 20mm (Sustrato MDF 18mm + HPL 0.9mm)

DXF CNC

FRENTE CAJÓN 2 MEDIO (B)

1 UN 20mm (HPL s/ MDF 18mm)



Frente HPL 20mm (Sustrato MDF 18mm + HPL 0.9mm)

DXF CNC

DETALLE 1 [redacted]
FONDO ESTRUCTURAL
Melamina 20mm • Placa maciza

DETALLE 2 [redacted]
ENSAMBLE ESTRUCTURAL
Minifix 34mm + Tarugo

DETALLE 3 [redacted]
CAZOLETA BISAGRA
Eje a 22.5mm • A 90mm ext.

DETALLE 4 [redacted]
SOPORTE REPISA
Pernos anti-vuelco

PROYECTO COCINA ARQUIFY

CLIENTE: CLIENTE PARTICULAR
LÁMINA: PLANOS DE FABRICACIÓN: MUEBLE BASE
CONTENIDO: MUEBLE BASE [CASCO S/ BASTIDOR] (450x600x600 mm) [PARTE 1/3]

DIBUJANTE: ARQUIFY BIM CAD FECHA: 24/10/2026

OBSERVACIONES CLÍNICAS MC.2.02

- **CAJAS:** MDF 15mm laminado blanco 2 caras con TC PVC 22x0.45mm
- **FRENTES:** MDF 18mm laminado blanco 2 caras con TC PVC 22x2.0mm PUR
- **ADHESIVO:** Poliuretano Reactivo (PUR) estanco anti-humedad

Correderas: **Rieles Telescópicos (13mm c/lado)** • Base de cajón: 364mm encajada entre laterales

NOMENCLATURA DE COTAS

- GENERAL
- TARUGO
- DETALLES / EJES
- MINIFIX

IDENT. ETIQ. **B-1**

LÁMINA: 03 / 17
ESCALA: S.E (A3)

arquify


NV-CAB_1 - COCINA MODULAR

MUEBLE BASE B-1 (TOTAL: 450 X 900 X 600 MM | CASCO: 450 X 600 X 570 MM)


Estructura: Abet Laminati / Provelcar Blanco Interni (HPL 0.9mm + Sustrato MDF 18mm -> Espesor final 20mm) **Frentes:** Abet Laminati / Provelcar Blanco Interni (HPL 0.9mm + Sustrato MDF 18mm -> Espesor final 20mm)

Trasera: Abet Laminati / Provelcar Blanco Interni (HPL 0.9mm + Sustrato MDF 18mm -> Espesor final 20mm)


VISTA DE PLANTA

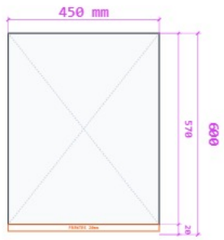

VISTA FRONTAL

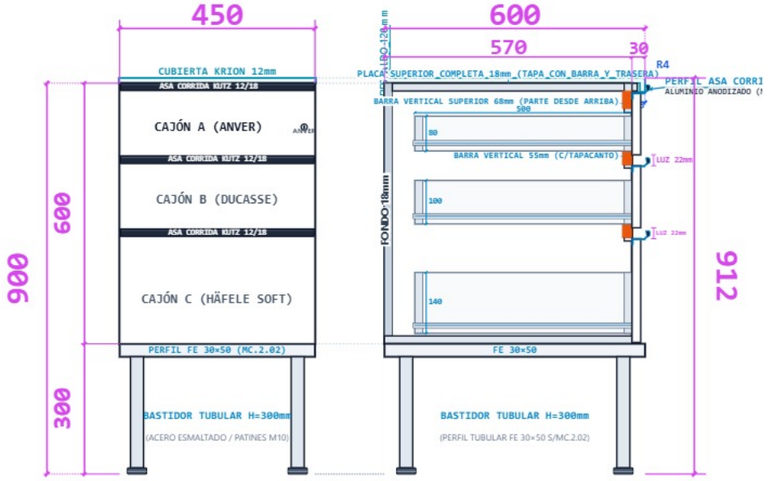


VISTA LATERAL

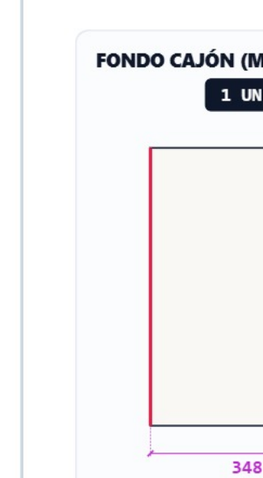

FRENTE CAJÓN 1 SUPERIOR (A)

1 UN 20mm (HPL s/ MDF 18mm)

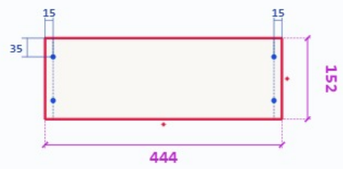


Frente HPL 20mm (Sustrato MDF 18mm + HPL 0.9mm)

DXF CNC

LATERAL CAJÓN (3 - INFERIOR)

2 UN 18mm

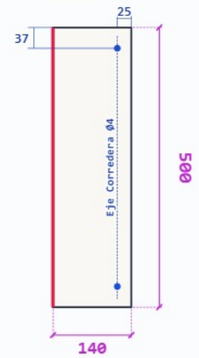


P/ Rieles Telescópicos Ext. Total (13mm c/lado) (NL=500mm)

DXF CNC

CONTRAFRENTE CAJÓN (3 -

1 UN 18mm

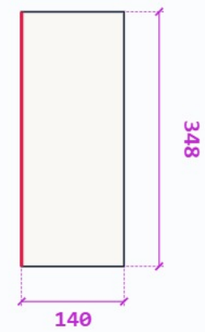


Testero frontal interior (descuenta 36mm laterales). Ancho ext. caja armada = 384mm (Rieles 13mm c/lado)

DXF CNC

TRASERA CAJÓN (3 - INFERIOR)

1 UN 18mm

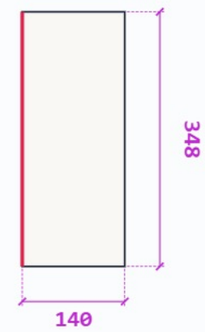


Testero posterior interior (descuenta 36mm laterales). Ancho ext. caja armada = 384mm (Rieles 13mm c/lado)

DXF CNC

FONDO CAJÓN (MDF 18MM HPL) (3 -

1 UN 18mm

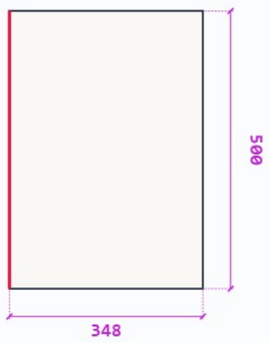


Fondo estructurado MDF 18mm laminado HPL 2 caras encajado entre laterales (348mm | caja ext. 384mm)

DXF CNC

LATERAL CAJÓN (2 - MEDIO)

2 UN 18mm

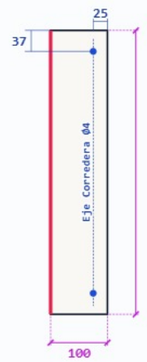


P/ Rieles Telescópicos Ext. Total (13mm c/lado) (NL=500mm)

DXF CNC

CONTRAFRENTE CAJÓN (2 - MEDIO)

1 UN 18mm

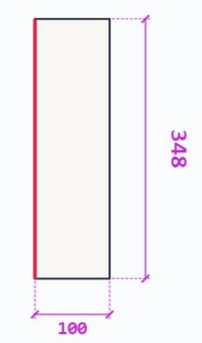


Testero frontal interior (descuenta 36mm laterales). Ancho ext. caja armada = 384mm (Rieles 13mm c/lado)

DXF CNC

TRASERA CAJÓN (2 - MEDIO)

1 UN 18mm

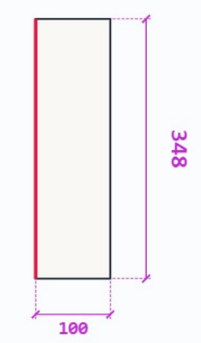

Testero posterior interior (descuenta 36mm laterales). Ancho ext. caja armada = 384mm (Rieles 13mm c/lado)

DXF CNC

DETALLE 1
FONDO ESTRUCTURAL
Melamina 20mm • Placa maciza

DETALLE 2
ENSAMBLE ESTRUCTURAL
Minifix 34mm + Tarugo

DETALLE 3
CAZOLETA BISAGRA
Eje a 22.5mm • A 90mm ext.

DETALLE 4
SOPORTE REPISA
Pernos anti-vuelco

PROYECTO COCINA ARQUIFY

CLIENTE: CLIENTE PARTICULAR
LÁMINA: PLANOS DE FABRICACIÓN: MUEBLE BASE
CONTENIDO: MUEBLE BASE [CASCO S/ BASTIDOR] (450x600x600 mm) [PARTE 2/3]

DIBUJANTE: ARQUIFY BIM CAD FECHA: 24/10/2026

OBSERVACIONES CLÍNICAS MC.2.02

- **CAJAS:** MDF 15mm laminado blanco 2 caras con TC PVC 22x0.45mm
- **FRENTES:** MDF 18mm laminado blanco 2 caras con TC PVC 22x2.0mm PUR
- **ADHESIVO:** Poliuretano Reactivo (PUR) estanco anti-humedad

Correderas: **Rieles Telescópicos (13mm c/lado)** • Base de cajón: 364mm encajada entre laterales

NOMENCLATURA DE COTAS

GENERAL · TARUGO · DETALLES / EJES · MINIFIX

IDENT. ETIQ. **B-1**

LÁMINA: 04 / 17
ESCALA: S.E (A3)

arquify


NV-CAB_1 - COCINA MODULAR

MUEBLE BASE B-1 (TOTAL: 450 X 900 X 600 MM | CASCO: 450 X 600 X 570 MM)


Estructura: Abet Laminati / Provelcar Blanco Interni (HPL 0.9mm + Sustrato MDF 18mm -> Espesor final 20mm) **Frentes:** Abet Laminati / Provelcar Blanco Interni (HPL 0.9mm + Sustrato MDF 18mm -> Espesor final 20mm)

Trasera: Abet Laminati / Provelcar Blanco Interni (HPL 0.9mm + Sustrato MDF 18mm -> Espesor final 20mm)

VISTA DE PLANTA

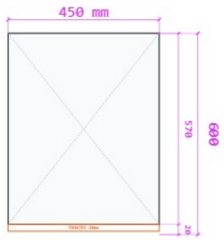

VISTA FRONTAL

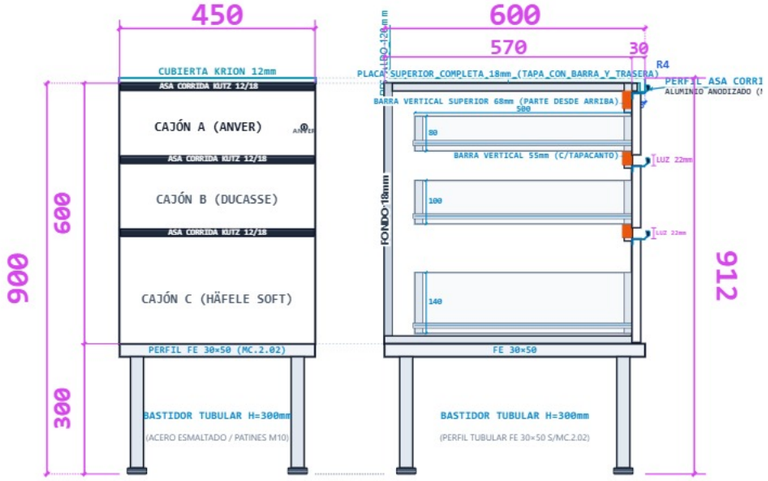


VISTA LATERAL



FONDO CAJÓN (MDF 18MM HPL) (2 -

1 UN 18mm

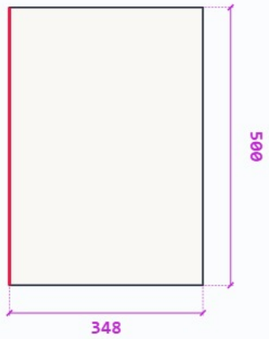


Fondo estructurado MDF 18mm laminado HPL 2 caras encajado entre laterales (348mm | caja ext. 384mm)

DXF CNC

LATERAL CAJÓN (1 - SUPERIOR)

2 UN 18mm

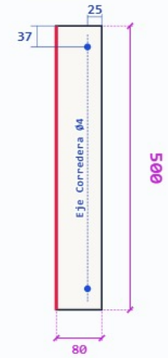

P/ Rieles Telescópicos Ext. Total (13mm c/lado) (NL=500mm)

DXF CNC

CONTRAFRENTE CAJÓN (1 -

1 UN 18mm



Testero frontal interior (descuenta 36mm laterales). Ancho ext. caja armada = 384mm (Rieles 13mm c/lado)

DXF CNC

TRASERA CAJÓN (1 - SUPERIOR)

1 UN 18mm




Testero posterior interior (descuenta 36mm laterales). Ancho ext. caja armada = 384mm (Rieles 13mm c/lado)

DXF CNC

FONDO CAJÓN (MDF 18MM HPL) (1 -

1 UN 18mm

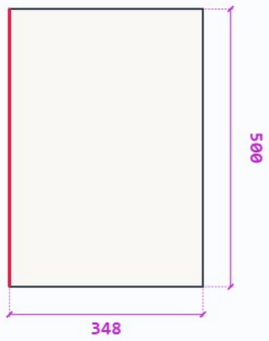

Fondo estructurado MDF 18mm laminado HPL 2 caras encajado entre laterales (348mm | caja ext. 384mm)

DXF CNC

DETALLE 1 [redacted]
FONDO ESTRUCTURAL
Melamina 20mm • Placa maciza

DETALLE 2 [redacted]
ENSAMBLE ESTRUCTURAL
Minifix 34mm + Tarugo

DETALLE 3 [redacted]
CAZOLETA BISAGRA
Eje a 22.5mm • A 90mm ext.

DETALLE 4 [redacted]
SOPORTE REPISA
Pernos anti-vuelco

PROYECTO COCINA ARQUIFY

CLIENTE: CLIENTE PARTICULAR
LÁMINA: PLANOS DE FABRICACIÓN: MUEBLE BASE
CONTENIDO: MUEBLE BASE [CASCO S/ BASTIDOR] (450x600x600 mm) [PARTE 3/3]

DIBUJANTE: ARQUIFY BIM CAD FECHA: 24/10/2026

OBSERVACIONES CLÍNICAS MC.2.02

- **CAJAS:** MDF 15mm laminado blanco 2 caras con TC PVC 22x0.45mm
- **FRENTES:** MDF 18mm laminado blanco 2 caras con TC PVC 22x2.0mm PUR
- **ADHESIVO:** Poliuretano Reactivo (PUR) estanco anti-humedad

Correderas: **Rieles Telescópicos (13mm c/lado)** • Base de cajón: 364mm encajada entre laterales

NOMENCLATURA DE COTAS

GENERAL · TARUGO · DETALLES / EJES · MINIFIX

IDENT. ETIQ. B-1

LÁMINA: 05 / 17
ESCALA: S.E (A3)

arquify


NV-CAB_1 - COCINA MODULAR

MUEBLE BASE B-2 (TOTAL: 900 X 900 X 600 MM | CASCO: 900 X 600 X 570 MM)


Estructura: Abet Laminati / Provelcar Blanco Interni (HPL 0.9mm + Sustrato MDF 18mm -> Espesor final 20mm) **Frentes:** Abet Laminati / Provelcar Blanco Interni (HPL 0.9mm + Sustrato MDF 18mm -> Espesor final 20mm)

Trasera: Abet Laminati / Provelcar Blanco Interni (HPL 0.9mm + Sustrato MDF 18mm -> Espesor final 20mm)

VISTA DE PLANTA

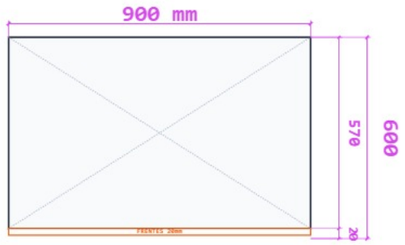


VISTA FRONTAL

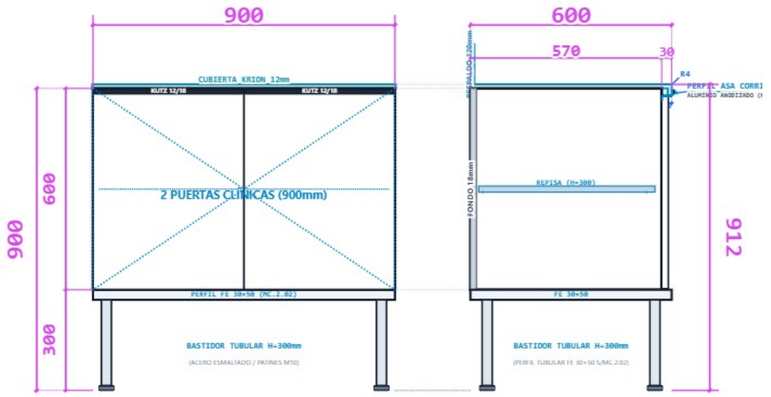

VISTA LATERAL

LATERAL

2 UN 18mm

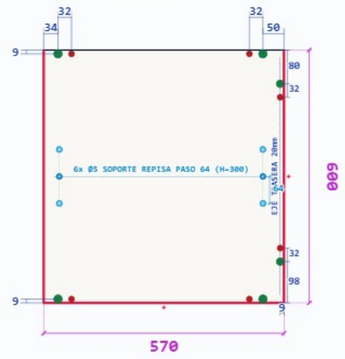


Laterales del gabinete

DXF CNC

PISO

1 UN 18mm

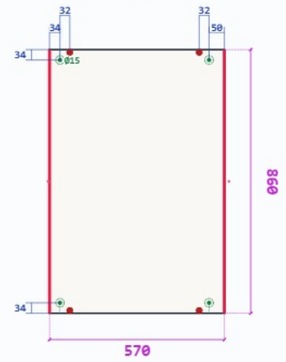


Piso del gabinete con sellado higiénico frontal y posterior (Bastidor metálico MC.2.02)

DXF CNC

TAPA SUPERIOR COMPLETA

1 UN 18mm

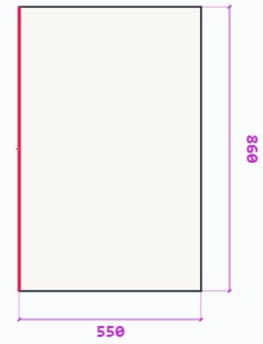


Placa superior completa de melamina para soporte higiénico de cubierta clínica (MC.2.02)

DXF CNC

FONDO TRASERA (MDF 18MM HPL)

1 UN 20mm

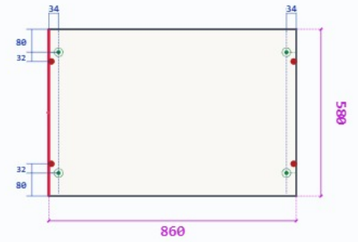


Tapa trasera de melamina/HPL 20mm que parte desde la cara superior del piso hasta la cota superior

DXF CNC

REPISA

1 UN 18mm (HPL s/ MDF 18mm)

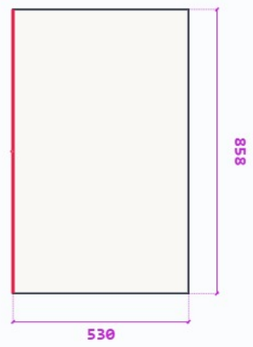


1 repisa(s) interior(es) regulable(s)

DXF CNC

PUERTA FRONTAL CLÍNICA (KUTZ)

2 UN 20mm (HPL s/ MDF 18mm)

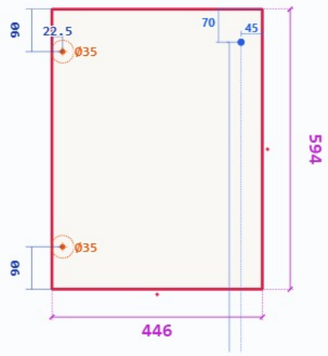

Puertas batientes clínicas de 2 hojas simétricas con perfil tirador KUTZ 12/18 y bisagras con freno

DXF CNC

DETALLE 1 [redacted]
FONDO ESTRUCTURAL
Melamina 20mm • Placa maciza

DETALLE 2 [redacted]
ENSAMBLE ESTRUCTURAL
Minifix 34mm + Tarugo

DETALLE 3 [redacted]
CAZOLETA BISAGRA
Eje a 22.5mm • A 90mm ext.

DETALLE 4 [redacted]
SOPORTE REPISA
Pernos anti-vuelco

PROYECTO COCINA ARQUIFY

CLIENTE: CLIENTE PARTICULAR
LÁMINA: PLANOS DE FABRICACIÓN: MUEBLE BASE
CONTENIDO: MUEBLE BASE [CASCO S/ BASTIDOR] (900x600x600 mm)

DIBUJANTE: ARQUIFY BIM CAD FECHA: 24/10/2026

OBSERVACIONES CLÍNICAS MC.2.02

- **CAJAS:** MDF 15mm laminado blanco 2 caras con TC PVC 22x0.45mm
- **FRENTES:** MDF 18mm laminado blanco 2 caras con TC PVC 22x2.0mm PUR
- **ADHESIVO:** Poliuretano Reactivo (PUR) estanco anti-humedad

Correderas: **Rieles Telescópicos (13mm c/lado)** • Base de cajón: 364mm encajada entre laterales

NOMENCLATURA DE COTAS

- GENERAL
- TARUGO
- DETALLES / EJES
- MINIFIX

IDENT. ETIQ. **B-2**

LÁMINA: 06 / 17
ESCALA: S.E (A3)

arquify


NV-CAB_1 - COCINA MODULAR

MUEBLE BASE B-3 (TOTAL: 300 X 900 X 600 MM | CASCO: 300 X 600 X 570 MM)

Estructura: Abet Laminati / Provelcar Blanco Interni (HPL 0.9mm + Sustrato MDF 18mm -> Espesor final 20mm) **Frentes:** Abet Laminati / Provelcar Blanco Interni (HPL 0.9mm + Sustrato MDF 18mm -> Espesor final 20mm)


Trasera: Abet Laminati / Provelcar Blanco Interni (HPL 0.9mm + Sustrato MDF 18mm -> Espesor final 20mm)

VISTA DE PLANTA

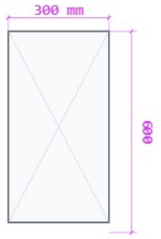


VISTA FRONTAL

VISTA LATERAL

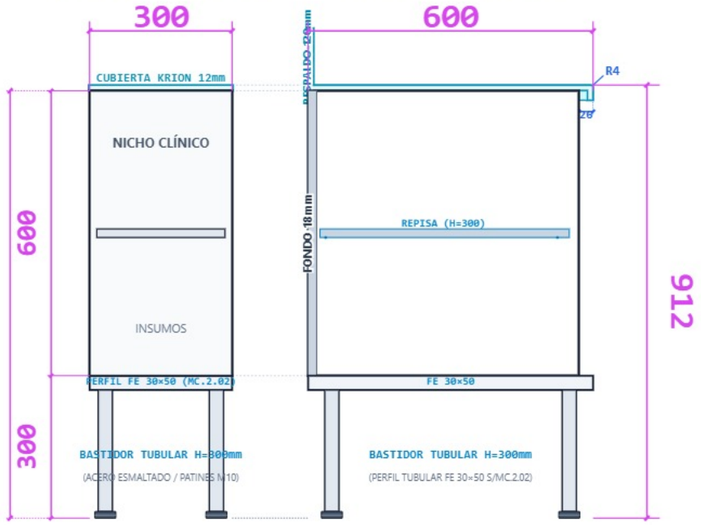

LATERAL

2 UN 18mm

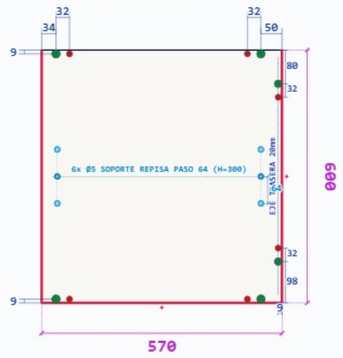


Laterales del gabinete

DXF CNC

PISO

1 UN 18mm

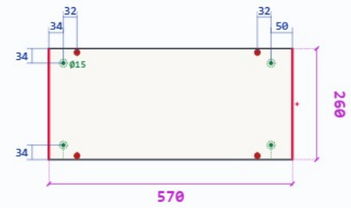


Piso del gabinete con sellado higiénico frontal y posterior (Bastidor metálico MC.2.02)

DXF CNC

TAPA SUPERIOR COMPLETA

1 UN 18mm

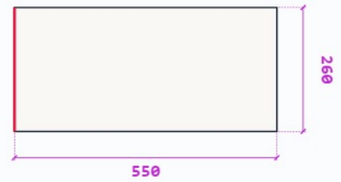


Placa superior completa de melamina para soporte higiénico de cubierta clínica (MC.2.02)

DXF CNC

FONDO TRASERA (MDF 18MM HPL)

1 UN 20mm

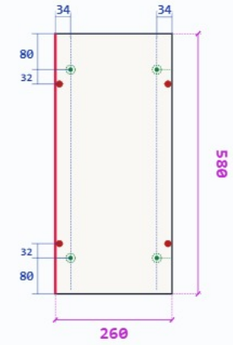


Tapa trasera de melamina/HPL 20mm que parte desde la cara superior del piso hasta la cota superior

DXF CNC

REPISA NICHO CLÍNICO

1 UN 18mm (HPL s/ MDF 18mm)

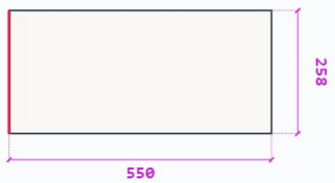

1 repisa vista interior para instrumental / dispensadores clínicos

DXF CNC

DETALLE 1 [redacted]
FONDO ESTRUCTURAL
Melamina 20mm • Placa maciza

DETALLE 2 [redacted]
ENSAMBLE ESTRUCTURAL
Minifix 34mm + Tarugo

DETALLE 3 [redacted]
CAZOLETA BISAGRA
Eje a 22.5mm • A 90mm ext.

DETALLE 4 [redacted]
SOPORTE REPISA
Pernos anti-vuelco

PROYECTO COCINA ARQUIFY

CLIENTE: CLIENTE PARTICULAR
LÁMINA: PLANOS DE FABRICACIÓN: MUEBLE BASE
CONTENIDO: MUEBLE BASE [CASCO S/ BASTIDOR] (300x600x600 mm)

DIBUJANTE: ARQUIFY BIM CAD FECHA: 24/10/2026

OBSERVACIONES CLÍNICAS MC.2.02

- **CAJAS:** MDF 15mm laminado blanco 2 caras con TC PVC 22x0.45mm
- **FRENTES:** MDF 18mm laminado blanco 2 caras con TC PVC 22x2.0mm PUR
- **ADHESIVO:** Poliuretano Reactivo (PUR) estanco anti-humedad

Correderas: **Rieles Telescópicos (13mm c/lado)** • Base de cajón: 364mm encajada entre laterales

NOMENCLATURA DE COTAS

- GENERAL
- TARUGO
- DETALLES / EJES
- MINIFIX

IDENT. ETIQ. B-3


LÁMINA: 07 / 17
ESCALA: S.E (A3)

arquify

ESQUEMA DE CORTE & OPTIMIZACIÓN #1

MATERIAL: **ABET LAMINATI / PROVELCAR BLANCO INTERNI (LAMINADO HPL 2 CARAS)** • FORMATO: **3050 X 1300 X 0.9 MM**

APROVECHAMIENTO
88.4%

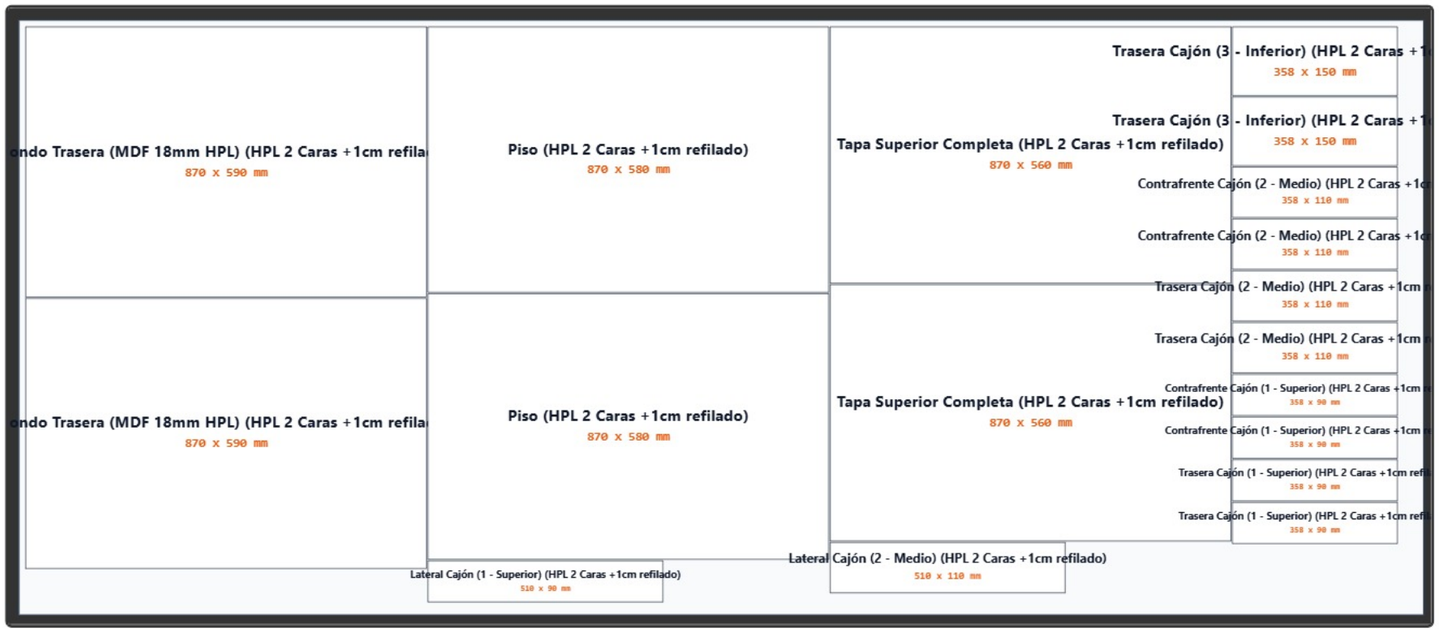

Formato Plancha: 3050 x 1300 mm **Espesor Hoja Sierra:** 3.2 mm **Margen Refilado:** 15 mm **Total Piezas Plancha:** 18 un.

PROYECTO COCINA ARQUIFY

CLIENTE: CLIENTE PARTICULAR
LÁMINA: OPTIMIZACIÓN CORTE: PLANCHA LAMINADO HPL 0.9MM (ABET LAMINATI 2 CARAS) - COLOR: Abet
CONTENIDO: PATRÓN #1 DE 7 (PLANCHA #1) - Abet Laminati / Provelcar Blanco Interni (Laminado HPL 2 Cara

DIBUJANTE: ARQUIFY BIM CAD FECHA: 24/10/2026

PARÁMETROS DE SECCIONADO & CORTE

- **ESPESOR SIERRA (KERF):** 3.2 mm (Disco con incisor)
- **REFILADO PERIMETRAL:** 15 mm mínimo por lado
- **SENTIDO DE VETA:** Longitudinal en frentes y tapas vistas

Algoritmo: **Guillotina 2D CAD/CAM**

CONVENCIONES DE CORTE

PIEZA ÚTIL
LÍNEA CORTE
RETAZO / MERMA
TAPACANTO
DIRECCIÓN VETA ↔ LONGITUDINAL

IDENT. ETIQ.
OPT-1

LÁMINA: 08 / 17
ESCALA: S.E (A3)

arquify

ESQUEMA DE CORTE & OPTIMIZACIÓN #2

MATERIAL: **ABET LAMINATI / PROVELCAR BLANCO INTERNI (LAMINADO HPL 2 CARAS)** • FORMATO: **3050 X 1300 X 0.9 MM**

APROVECHAMIENTO
90.6%



Formato Plancha: 3050 x 1300 mm **Espesor Hoja Sierra:** 3.2 mm **Margen Refilado:** 15 mm **Total Piezas Plancha:** 14 un.

PROYECTO COCINA ARQUIFY

CLIENTE: CLIENTE PARTICULAR
LÁMINA: OPTIMIZACIÓN CORTE: PLANCHA LAMINADO HPL 0.9MM (ABET LAMINATI 2 CARAS) - COLOR: Abet
CONTENIDO: PATRÓN #2 DE 7 (PLANCHA #2) - Abet Laminati / Provelcar Blanco Interni (Laminado HPL 2 Cara

DIBUJANTE: ARQUIFY BIM CAD FECHA: 24/10/2026

PARÁMETROS DE SECCIONADO & CORTE

- **ESPESOR SIERRA (KERF):** 3.2 mm (Disco con incisor)
- **REFILADO PERIMETRAL:** 15 mm mínimo por lado
- **SENTIDO DE VETA:** Longitudinal en frentes y tapas vistas

Algoritmo: **Guillotina 2D CAD/CAM**

CONVENCIONES DE CORTE

PIEZA ÚTIL
LÍNEA CORTE
RETAZO / MERMA
TAPACANTO
DIRECCIÓN VETA ↔ LONGITUDINAL

IDENT. ETIQ.
OPT-2


LÁMINA: 09 / 17
ESCALA: S.E (A3)

arquify

ESQUEMA DE CORTE & OPTIMIZACIÓN #3

MATERIAL: **ABET LAMINATI / PROVELCAR BLANCO INTERNI (LAMINADO HPL 2 CARAS)** • FORMATO: **3050 X 1300 X 0.9 MM**

APROVECHAMIENTO
88.9%

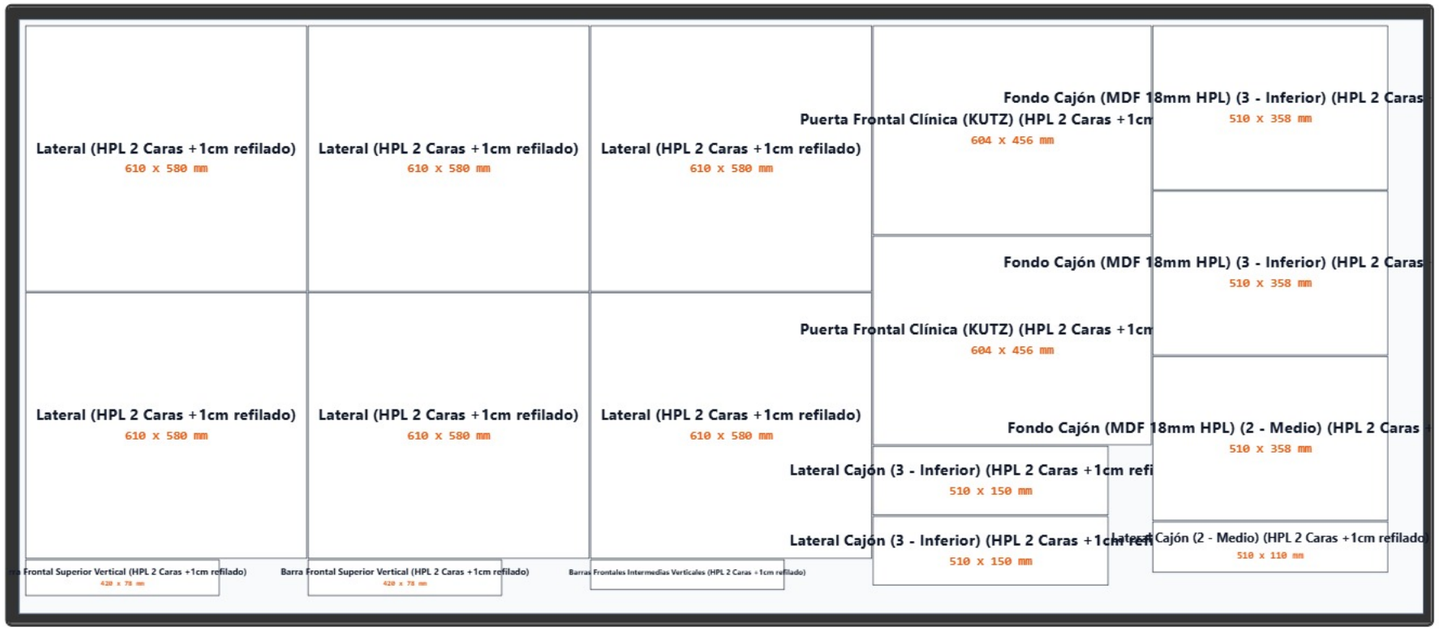

Formato Plancha: 3050 x 1300 mm **Espesor Hoja Sierra:** 3.2 mm **Margen Refilado:** 15 mm **Total Piezas Plancha:** 17 un.

PROYECTO COCINA ARQUIFY

CLIENTE: CLIENTE PARTICULAR
LÁMINA: OPTIMIZACIÓN CORTE: PLANCHA LAMINADO HPL 0.9MM (ABET LAMINATI 2 CARAS) - COLOR: Abet
CONTENIDO: PATRÓN #3 DE 7 (PLANCHA #3) - Abet Laminati / Provelcar Blanco Interni (Laminado HPL 2 Cara

DIBUJANTE: ARQUIFY BIM CAD FECHA: 24/10/2026

PARÁMETROS DE SECCIONADO & CORTE

- **ESPESOR SIERRA (KERF):** 3.2 mm (Disco con incisor)
- **REFILADO PERIMETRAL:** 15 mm mínimo por lado
- **SENTIDO DE VETA:** Longitudinal en frentes y tapas vistas

Algoritmo: **Guillotina 2D CAD/CAM**

CONVENCIONES DE CORTE

PIEZA ÚTIL
RETAZO / MERMA
LÍNEA CORTE
TAPACANTO
DIRECCIÓN VETA ↔ LONGITUDINAL

IDENT. ETIQ.
OPT-3


LÁMINA: 10 / 17
ESCALA: S.E (A3)

arquify

ESQUEMA DE CORTE & OPTIMIZACIÓN #4

MATERIAL: **ABET LAMINATI / PROVELCAR BLANCO INTERNI (LAMINADO HPL 2 CARAS)** • FORMATO: **3050 X 1300 X 0.9 MM**

APROVECHAMIENTO
85.8%

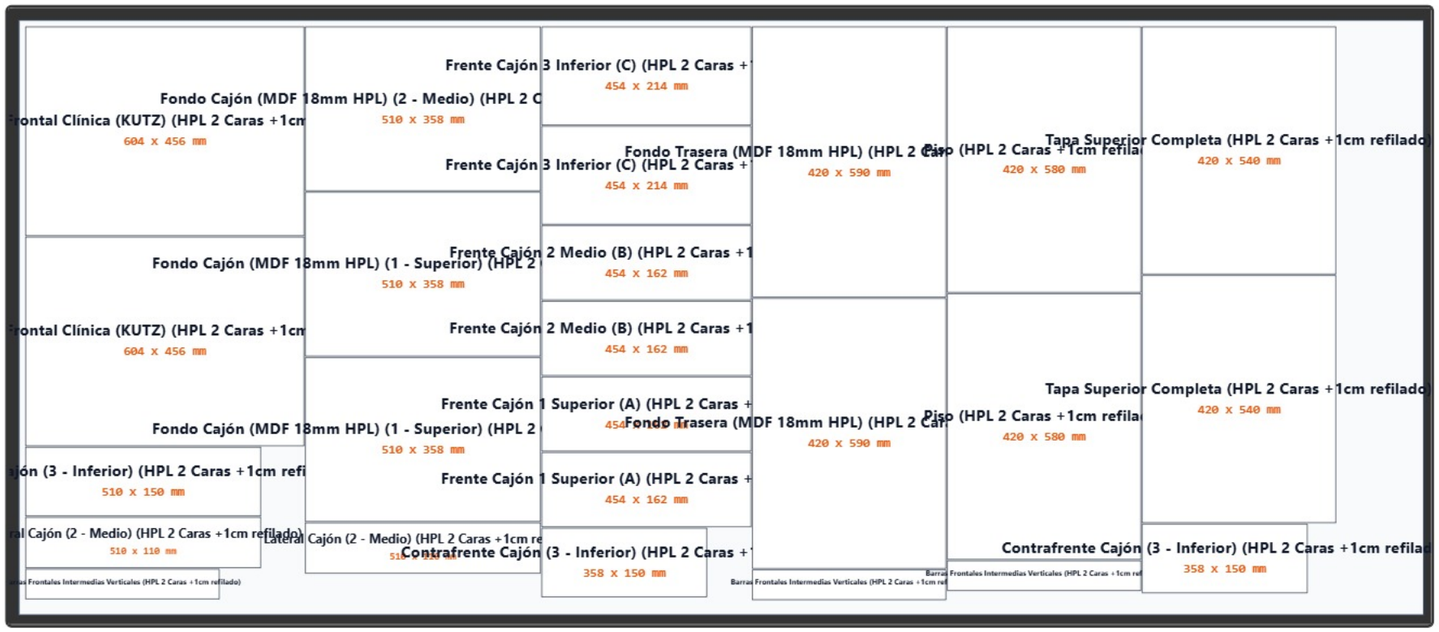

Formato Plancha: 3050 x 1300 mm **Espesor Hoja Sierra:** 3.2 mm **Margen Refilado:** 15 mm **Total Piezas Plancha:** 25 un.

PROYECTO COCINA ARQUIFY

CLIENTE: CLIENTE PARTICULAR
LÁMINA: OPTIMIZACIÓN CORTE: PLANCHA LAMINADO HPL 0.9MM (ABET LAMINATI 2 CARAS) - COLOR: Abet
CONTENIDO: PATRÓN #4 DE 7 (PLANCHA #4) - Abet Laminati / Provelcar Blanco Interni (Laminado HPL 2 Cara

DIBUJANTE: ARQUIFY BIM CAD FECHA: 24/10/2026

PARÁMETROS DE SECCIONADO & CORTE

- **ESPESOR SIERRA (KERF):** 3.2 mm (Disco con incisor)
- **REFILADO PERIMETRAL:** 15 mm mínimo por lado
- **SENTIDO DE VETA:** Longitudinal en frentes y tapas vistas

Algoritmo: **Guillotina 2D CAD/CAM**

CONVENCIONES DE CORTE

- PIEZA ÚTIL
- RETAZO / MERMA
- LÍNEA CORTE
- TAPACANTO

DIRECCIÓN VETA ⇔ LONGITUDINAL

IDENT. ETIQ.
OPT-4

LÁMINA: 11 / 17
ESCALA: S.E (A3)

arquify

ESQUEMA DE CORTE & OPTIMIZACIÓN #5

MATERIAL: **ABET LAMINATI / PROVELCAR BLANCO INTERNI (LAMINADO HPL 2 CARAS)** • FORMATO: **3050 X 1300 X 0.9 MM**

APROVECHAMIENTO
23.1%



Formato Plancha: 3050 x 1300 mm **Espesor Hoja Sierra:** 3.2 mm **Margen Refilado:** 15 mm **Total Piezas Plancha:** 6 un.

PROYECTO COCINA ARQUIFY

CLIENTE: CLIENTE PARTICULAR
LÁMINA: OPTIMIZACIÓN CORTE: PLANCHA LAMINADO HPL 0.9MM (ABET LAMINATI 2 CARAS) - COLOR: Abet
CONTENIDO: PATRÓN #5 DE 7 (PLANCHA #5) - Abet Laminati / Provelcar Blanco Interni (Laminado HPL 2 Cara

DIBUJANTE: ARQUIFY BIM CAD FECHA: 24/10/2026

PARÁMETROS DE SECCIONADO & CORTE

- **ESPESOR SIERRA (KERF):** 3.2 mm (Disco con incisor)
- **REFILADO PERIMETRAL:** 15 mm mínimo por lado
- **SENTIDO DE VETA:** Longitudinal en frentes y tapas vistas

Algoritmo: **Guillotina 2D CAD/CAM**

CONVENCIONES DE CORTE

PIEZA ÚTIL
RETAZO / MERMA
LÍNEA CORTE
TAPACANTO
DIRECCIÓN VETA ⇔ LONGITUDINAL

IDENT. ETIQ.
OPT-5

LÁMINA: 12 / 17
ESCALA: S.E (A3)


arquify

PATRÓN #6 DE 7 (2 PLANCHAS TOTALES)

ESQUEMA DE CORTE & OPTIMIZACIÓN #6

MATERIAL: **MDF CRUDO 18MM (SUSTRATO BASE)** • FORMATO: 2440 X 1830 X 18 MM

APROVECHAMIENTO
82.1%

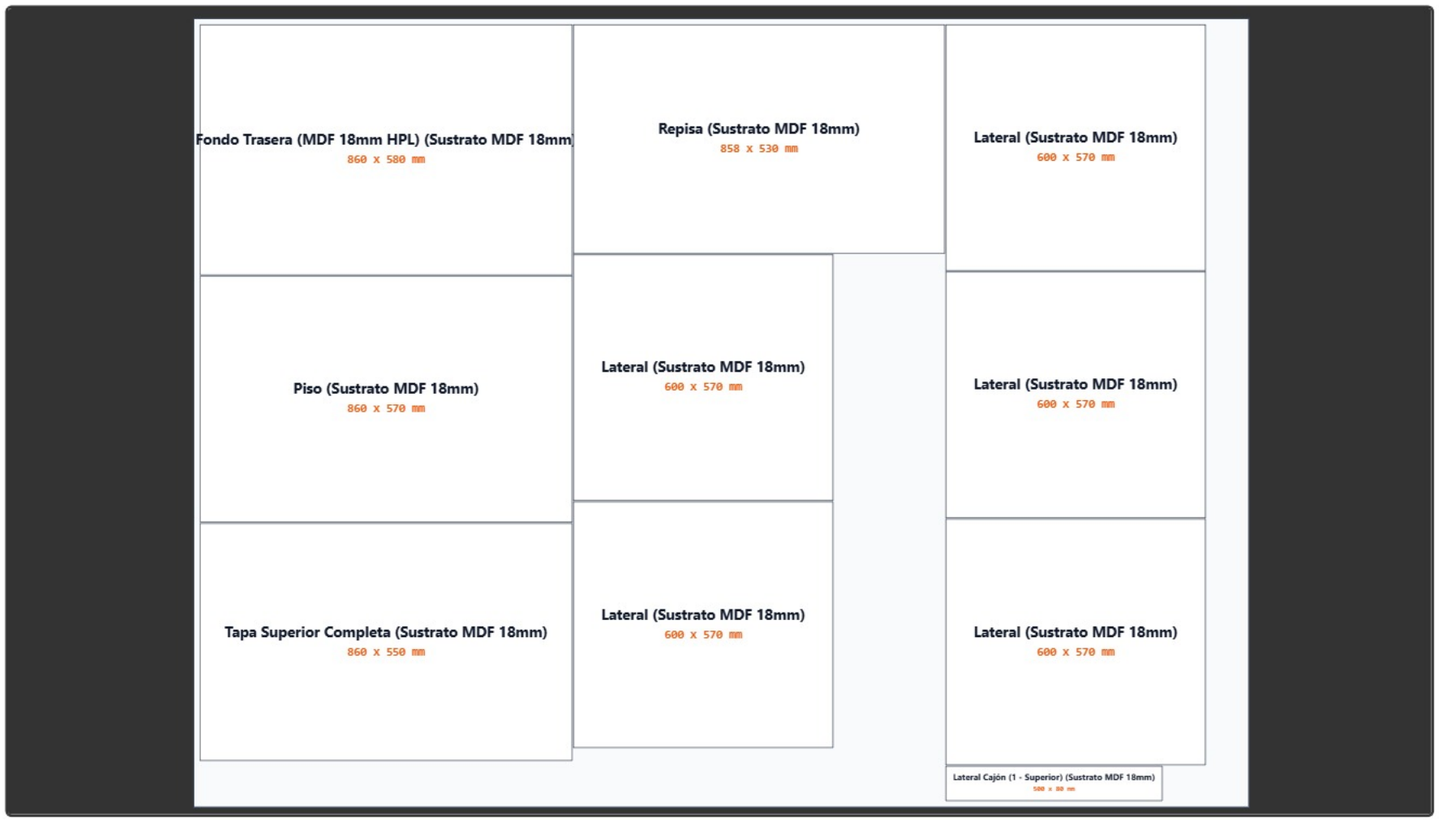

Formato Plancha: 2440 x 1830 mm **Espesor Hoja Sierra:** 3.2 mm **Margen Refilado:** 15 mm **Total Piezas Plancha:** 10 un.

PROYECTO COCINA ARQUIFY

CLIENTE: CLIENTE PARTICULAR
LÁMINA: OPTIMIZACIÓN CORTE: PLANCHA MDF CRUDO 18MM (SUSTRATO ESTRUCTURA, PUERTAS Y CAJONI
CONTENIDO: PATRÓN #6 DE 7 (PLANCHA #6) - MDF Crudo 18mm (Sustrato Base) 18mm

DIBUJANTE: ARQUIFY BIM CAD FECHA: 24/10/2026

PARÁMETROS DE SECCIONADO & CORTE

- **ESPESOR SIERRA (KERF):** 3.2 mm (Disco con incisor)
- **REFILADO PERIMETRAL:** 15 mm mínimo por lado
- **SENTIDO DE VETA:** Longitudinal en frentes y tapas vistas

Algoritmo: **Guillotina 2D CAD/CAM**

CONVENCIONES DE CORTE

PIEZA ÚTIL
LÍNEA CORTE
RETAZO / MERMA
TAPACANTO
DIRECCIÓN VETA ↔ LONGITUDINAL

IDENT. ETIQ.
OPT-6

LÁMINA: 13 / 17
ESCALA: S.E (A3)


arquify

PATRÓN #7 DE 7 (2 PLANCHAS TOTALES)

ESQUEMA DE CORTE & OPTIMIZACIÓN #7

MATERIAL: **MDF CRUDO 18MM (SUSTRATO BASE)** • FORMATO: `2440 X 1830 X 18 MM`

APROVECHAMIENTO
77.7%

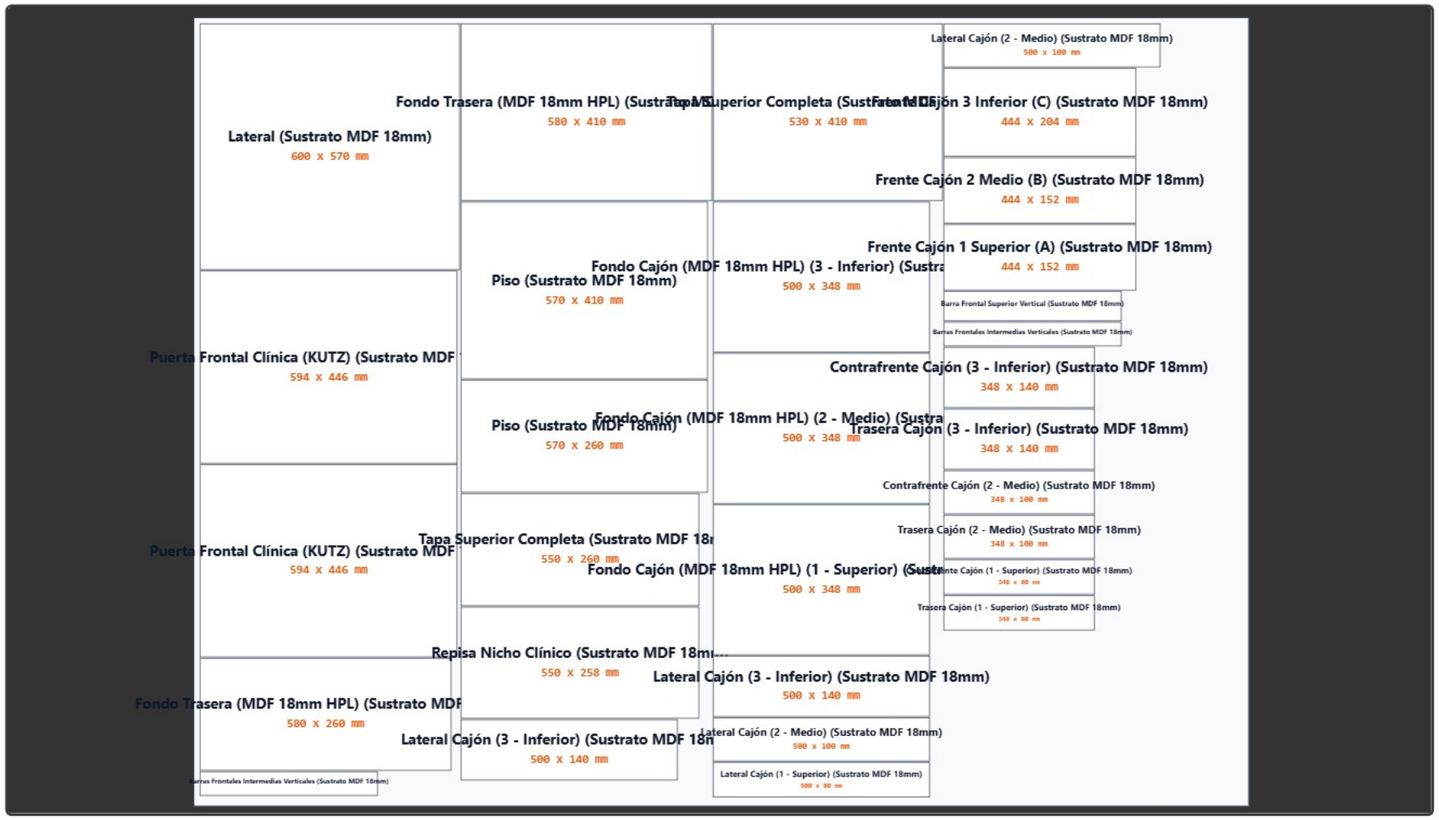

Formato Plancha: 2440 x 1830 mm **Espesor Hoja Sierra:** 3.2 mm **Margen Refilado:** 15 mm **Total Piezas Plancha:** 30 un.

PROYECTO COCINA ARQUIFY

CLIENTE: CLIENTE PARTICULAR
LÁMINA: OPTIMIZACIÓN CORTE: PLANCHA MDF CRUDO 18MM (SUSTRATO ESTRUCTURA, PUERTAS Y CAJONI
CONTENIDO: PATRÓN #7 DE 7 (PLANCHA #7) - MDF Crudo 18mm (Sustrato Base) 18mm

DIBUJANTE: ARQUIFY BIM CAD FECHA: 24/10/2026

PARÁMETROS DE SECCIONADO & CORTE

- **ESPESOR SIERRA (KERF):** 3.2 mm (Disco con incisor)
- **REFILADO PERIMETRAL:** 15 mm mínimo por lado
- **SENTIDO DE VETA:** Longitudinal en frentes y tapas vistas

Algoritmo: **Guillotina 2D CAD/CAM**

CONVENCIONES DE CORTE

- PIEZA ÚTIL
- RETAZO / MERMA
- LÍNEA CORTE
- TAPACANTO

DIRECCIÓN VETA ⇔ LONGITUDINAL

IDENT. ETIQ.
OPT-7

LÁMINA: 14 / 17
ESCALA: S.E (A3)


arquify

PATRÓN #1 DE 1 (1 PLANCHAS TOTALES)

ESQUEMA DE CORTE & OPTIMIZACIÓN EN PLANCHA #1

MATERIAL: **KRION SOLID SURFACE BLANCO (1100 SNOW WHITE EAST 12MM)** • ESPESOR: **12 MM** • CRITERIO LOGÍSTICO: **CASA (MÁX 2500 MM)**

APROVECHAMIENTO
46%
Útil: 1.284 m² | Retazo: 1.513 m²

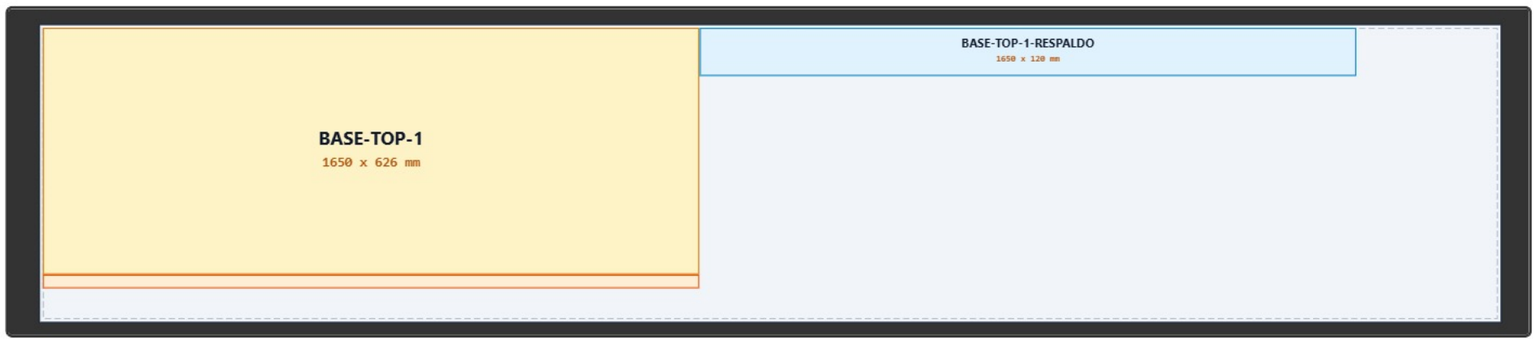

Formato Plancha: 3680 x 760 mm **Espesor Disco Diamante:** Kerf 3.5 mm **Despunte Perimetral:** 10 mm **Criterio Logístico:** Casa (máx 2500 mm)

Cubierta Faldón Respaldo Cascada Encastre

PROYECTO COCINA ARQUIFY

CLIENTE: CLIENTE PARTICULAR
LÁMINA: OPTIMIZACIÓN CUBIERTA KRION SOLID SURFACE BLANCO (1100 SNOW WHITE EAST 12MM): PLANC
CONTENIDO: Krion Solid Surface Blanco (1100 Snow White EAST 12mm)

DIBUJANTE: ARQUIFY BIM CAD FECHA: 24/10/2026

ESPECIFICACIONES DE CUBIERTA SANITARIA

- **MATERIAL:** Krion Solid Surface Snow White / HPL Compacto 12mm
- **TERMINACIÓN:** Canto macizo 12mm pulido sanitario sin filo
- **ASEPSIA:** Superficie no porosa, sin uniones perceptibles

Logística: **Largo máx. continuo 2.50m**

PIEZAS PÉTREAS QSTONE

- CUBIERTA / ISLA
- CASCADA LATERAL
- RETAJO APROVECHABLE
- FALDÓN FRONTAL
- RESPALDO MURO

IDENT. ETIQ.
QS-1

LÁMINA: 15 / 17
ESCALA: S.E (A3)

arquify

LISTADO CONSOLIDADO DE MATERIALES E INSUMOS (BOM)

SISTEMA: MINIFIX + TARUGO 8X30 • CORREDERAS: TELESCOPICA • TABLEROS FORMATO ESTÁNDAR

Ítems 1 - 15 de 21

CATEGORÍA	ÍTEM / COMPONENTE	CANTIDAD	UNIDAD	DETALLES DE APLICACIÓN
[redacted]	Plancha Laminado HPL (Abet Laminati / Provelcar Blanco Interni)	5	Planchas (3050x1300x0.9mm)	Área neta: 14.94 m² | Aprovechamiento est.: 75.4% (Patrón #1 + Patrón #2 + Patrón #3 + Patrón #4 + Patrón #5)
[redacted]	Plancha MDF Crudo / Sustrato Base p/ HPL (18mm)	2	Planchas (2440x1830x18mm)	Área neta: 7.13 m² | Aprovechamiento est.: 79.9% (Patrón #6 + Patrón #7)
[redacted]	Adhesivo de Contacto Alta Resistencia (Prensado HPL)	3	Litros / Galón	Pegado de alta resistencia HPL sobre sustrato MDF 18mm (14.3 m² caras)
[redacted]	Plancha Cubierta Krion Solid Surface Blanco (1100 Snow White EAST 12mm) (12mm)	1	Planchas (3680x760x12mm)	Área neta útil: 1.28 m² | Aprovechamiento est.: 46% (Patrón #1)
[redacted]	Adhesivo Bicomponente Krion® / Solid Surface (Tubo 250ml al tono)	2	Cartuchos	Pegado químico homogéneo sin poros ni juntas visibles (5.6 m lineales pulidos)
[redacted]	Sellador Elastomérico Fungicida Aséptico (Silicona Sanitaria)	1	Cartucho	Sellado perimetral posterior y estanqueidad contra muro
[redacted]	Tapacanto PVC Puertas y Frentes (22x1.00mm)	9	Metros Lineales	Terminación perimetral frentes (Abet Laminati / Provelcar Blanco Interni)
[redacted]	Tapacanto PVC Estructura (22x1.00mm)	30	Metros Lineales	Cantos frontales e interiores de gabinetes (Abet Laminati / Provelcar Blanco Interni)
[redacted]	Pernos Minifix + Cajas Excéntricas 15mm	60	Juegos	Estructura (60) + Cajones (0)
[redacted]	Tarugos de Madera 8x30mm	120	Unidades	Encastre y alineación estructural mecanizada
[redacted]	Tapas Adhesivas Embellecedoras para Minifix (Ø15mm)	60	Unidades	Ocultamiento estético de cajas excéntricas
[redacted]	Bisagras Cazoleta 35mm Rectas (Cierre Suave)	4	Unidades	Puertas exteriores de gabinetes y despensas
[redacted]	Tornillos Fijación Bisagras 3.5x16mm	16	Unidades	Para cazoleta y base de montaje
[redacted]	Soportes de Repisa Niquelados Ø5mm (Pitones con Retén/Goma)	8	Unidades	Montaje y fijación regulable de repisas interiores (2 repisas x 4 soportes)
ESTRUCTURA METÁLICA	Perfil Tubular FE 30x50x1.5mm Esmaltado Blanco (Barra 6m)	2	Barras	Estructura autoportante unificada según Plano Independiente MC.2.02 (1 bancada continua). Total: 6.46 m lineales de perfil tubular.

PROYECTO COCINA ARQUIFY

CLIENTE: CLIENTE PARTICULAR
LÁMINA: LISTADO CONSOLIDADO DE MATERIALES E INSUMOS (BOM) [1/2]
CONTENIDO: CÓMPUTO MÉTRICO, HERRAJES Y FIJACIONES (HOJA 1 DE 2)

DIBUJANTE: ARQUIFY BIM CAD — FECHA: 24/10/2026

CÓMPUTO MÉTRICO & HERRAJES CLÍNICOS

- **BASTIDOR FE:** Perfil tubular FE 30x50x1.5mm esmaltado blanco h=300mm
- **QUINCALLERÍA:** Cerradura Trampa ANVER + Tirador Perfil KUTZ 12/18
- **CORREDERAS:** Ducasse telescópicas A-B + Häfele cierre suave C

Lista Maestra: **Consolidado de Producción**

CONTROL DE FABRICACIÓN

ESTADO: **APROBADO** — REVISIÓN: **REV. A**
TOLERANCIA: **±0.5 mm** — NORMA: **ISO 128**
LISTA VINCULADA AL BOM

IDENT. ETIQ. BOM-01

LÁMINA: 16 / 17
ESCALA: S.E (A3)

arquify

[redacted]

LISTADO CONSOLIDADO DE MATERIALES E INSUMOS (BOM)

SISTEMA: MINIFIX + TARUGO 8X30 • CORREDERAS: TELESCOPICA • TABLEROS FORMATO ESTÁNDAR

Ítems 16 - 21 de 21

CATEGORÍA	ÍTEM / COMPONENTE	CANTIDAD	UNIDAD	DETALLES DE APLICACIÓN
[redacted]	Patín Regulador Nivelador Metálico Sanitario M10	6	Unidades	Patines reguladores para apoyo y nivelación de estructura tubular independiente (6 puntos de apoyo con base de goma antideslizante lavable).
[redacted]	Cerradura Trampa ANVER (Control Insumos / Medicamentos)	1	Unidades	Cerradura trampa de alta seguridad montada en cajón superior (Ficha Técnica MC.2.02 SACYR)
[redacted]	Corredera Telescópica 500mm sin cierre suave Ducasse (Cajones A-B)	2	Pares	Guías telescópicas pesadas Ducasse 500mm para cajones A y B
[redacted]	Corredera Telescópica 500mm con cierre suave Häfele (Cajón C)	1	Pares	Guías telescópicas pesadas Häfele 500mm con amortiguador integrado para gaveta inferior C
[redacted]	Perfil Tirador Asa Corrida KUTZ 12/18 (Negro Mate - Barra 3000mm / 3m)	1	Barras	Optimización de corte en barras de 3.00 m (2.22 m lineales netos, 5 cortes a medida total de frentes). Requiere mecanizado de rebaje 2×15mm en tablero 18mm.
[redacted]	Tornillos Autorroscantes 3.5x15mm para Perfil KUTZ	20	Unidades	Fijación de pestaña posterior embutida sobre rebaje de frentes

PROYECTO COCINA ARQUIFY

CLIENTE: CLIENTE PARTICULAR
LÁMINA: LISTADO CONSOLIDADO DE MATERIALES E INSUMOS (BOM) [2/2]
CONTENIDO: CÓMPUTO MÉTRICO, HERRAJES Y FIJACIONES (HOJA 2 DE 2)

DIBUJANTE: ARQUIFY BIM CAD FECHA: 24/10/2026

CÓMPUTO MÉTRICO & HERRAJES CLÍNICOS

- **BASTIDOR FE:** Perfil tubular FE 30x50x1.5mm esmaltado blanco h=300mm
- **QUINCALLERÍA:** Cerradura Trampa ANVER + Tirador Perfil KUTZ 12/18
- **CORREDERAS:** Ducasse telescópicas A-B + Häfele cierre suave C

Lista Maestra: **Consolidado de Producción**

CONTROL DE FABRICACIÓN

ESTADO: **APROBADO**
REVISIÓN: **REV. A**
TOLERANCIA: **±0.5 mm**
NORMA: **ISO 128**

LISTA VINCULADA AL BOM

IDENT. ETIQ.
BOM-02

LÁMINA: 17 / 17
ESCALA: S.E (A3)

arquify