
PROYECTO COCINA MODULAR ARQUIFY


PLANTA GENERAL Y ELEVACIONES (1 MÓDULO)

VISTA PLANTA GENERAL (ARQUITECTURA)

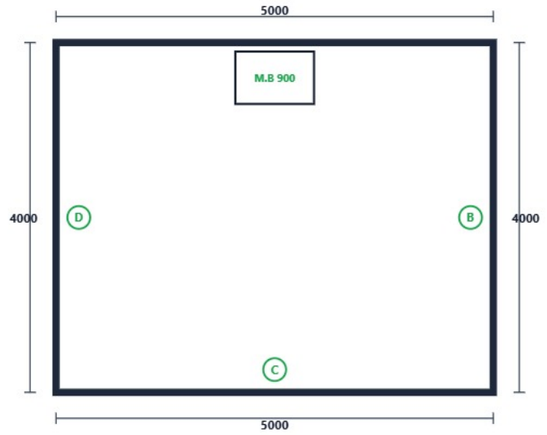

A VISTA FRONTAL A

L = 5000 mm

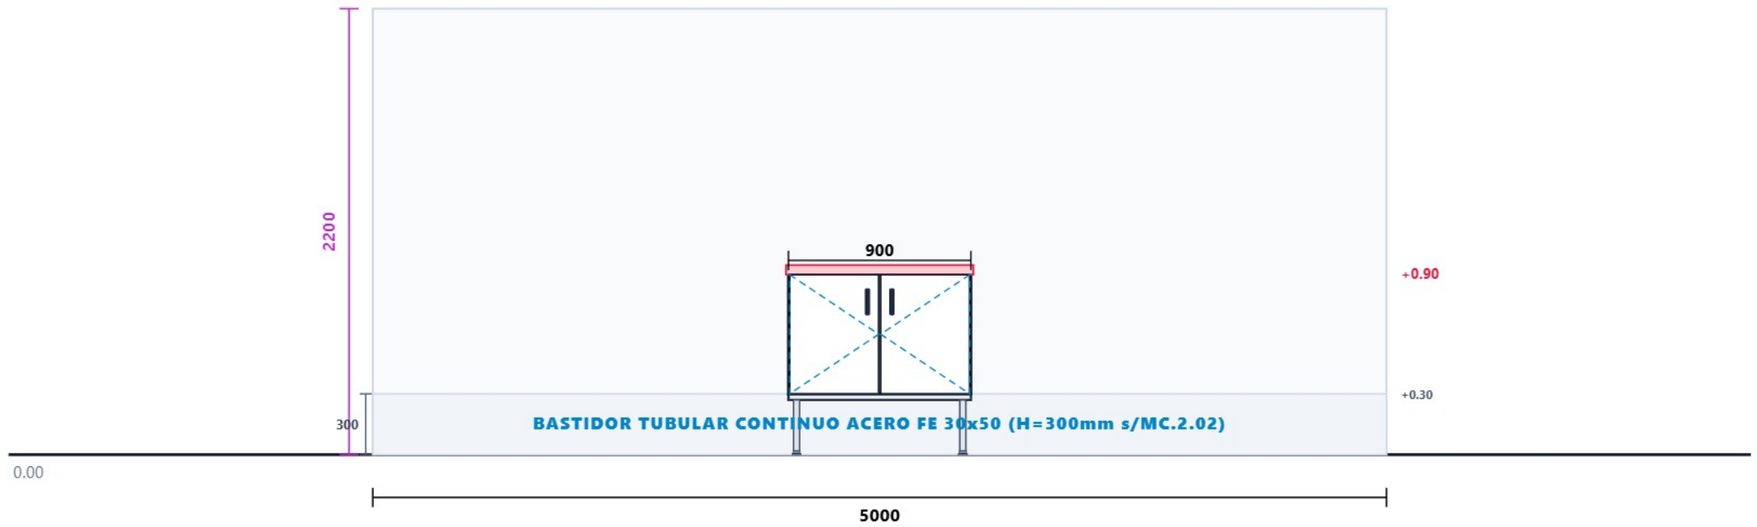

Zócalo H=300 mm | Murales con puertas y anclajes

Costados / Casco: Abet Laminati / Provelcar Blanco Interni

PROYECTO COCINA ARQUIFY

CLIENTE: CLIENTE PARTICULAR
LÁMINA: PROYECTO COCINA MODULAR ARQUIFY
CONTENIDO: PLANTA GENERAL Y ELEVACIONES

DIBUJANTE: ARQUIFY BIM CAD FECHA: 26/10/2026

ESPECIFICACIONES CLÍNICAS & ARQUITECTURA

- **NORMATIVA:** Ficha Técnica MC.2.02 SACYR • Mobiliario Clínico
- **BASTIDOR SANITARIO:** Tubular FE 30x50x1.5mm h=300 mm libres del suelo
- **NIVEL CUBIERTA:** N.P.T. +0.90 m | Krion Solid Surface 12mm

Normativa: **ISO 128 / NCh Arquitectura**

SIMBOLOGÍA DE PLANTA

- MURO / VISTA
- COTA TOTAL
- PROYECCIÓN AÉREOS
- COTA ALTURA
- NIVEL P.T.

IDENT. ETIQ. PL-01

LÁMINA: 01 / 10
ESCALA: 1:50 (A3)

arquify


LÁMINA DE FABRICACIÓN: BASTIDOR TUBULAR METÁLICO CONTINUO

Estructura autoportante unificada en FE 30×50×1.5mm (BLANCO EPÓXICO) + patines reguladores sanitarios M10 a 300mm del suelo.

ACABADO / MATERIAL: BLANCO EPÓXICO

CÓDIGO DE ELEMENTO: MC.2.02-EST

BANCADA BASTIDOR CONTINUO #1: L = 900 MM × P = 620 MM × H = 300 MM

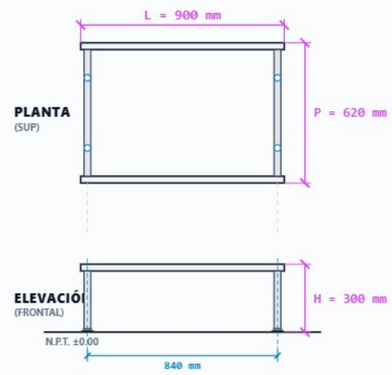



DESPIECE DE CORTES Y MATERIALES (HERRERÍA CLÍNICA / SACYR)

Total lineal acero: **3.86 m** • Barras 6m: **1 un**

Pieza / Perfil	Sección / Material	Cant. Unit.	Largo Unit.	Total Lineal	Corte / Acabado / Especificación
Larguero Longitudinal Frontal y Trasero	FE 30×50×1.5mm	**2**	900 mm	1.80 m	Corte a 90° escuadra. Tubo continuo sin empalmes. Tratamiento fosfatizado + Pintura electrostática epóxica al horno Blanco Puro RAL 9010.
Travesaños Transversales de Amarre	FE 30×50×1.5mm	**2**	520 mm	1.04 m	Soldadura continua pulida a ras. Perforación Ø6mm para fijación.
Fustes Verticales de Pata Tubular	FE 30×50×1.5mm	**4**	256 mm	1.02 m	Base sellada con pletina electrosoldada y tuerca embutida M10.
Patín Regulador Sanitario Nivelador	Rosca M10 × 40mm	**4**	H=14 (+15) mm	—	Vástago de acero M10 con base cilíndrica de goma antideslizante lavable.

NOTAS DE TALLER: 1. Soldadura continua bajo atmósfera controlada sin porosidad. 2. Todas las aristas y cordones exteriores deben quedar enrasados y desbastados con disco abrasivo grano 120/240. 3. Terminación: Pintura electrostática en polvo termoendurecible horneada a 200°C, color Blanco Epóxico Sanitario RAL 9010. **DESPEJE SANITARIO: 300 mm N.P.T.**


NV-CAB_1 - COCINA MODULAR

MUEBLE BASE B-1 (TOTAL: 900 X 888 X 600 MM | CASCO: 900 X 588 X 570 MM)


Estructura: Abet Laminati / Provelcar Blanco Interni (HPL 0.9mm + Sustrato MDF 18mm -> Espesor final 20mm) **Frentes:** Abet Laminati / Provelcar Blanco Interni (HPL 0.9mm + Sustrato MDF 18mm -> Espesor final 20mm)

Trasera: Abet Laminati / Provelcar Blanco Interni (HPL 0.9mm + Sustrato MDF 18mm -> Espesor final 20mm)

VISTA DE PLANTA

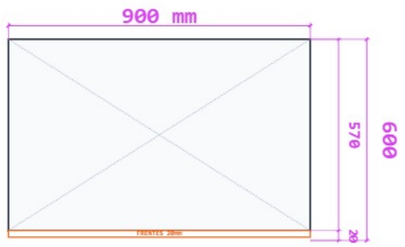

VISTA FRONTAL

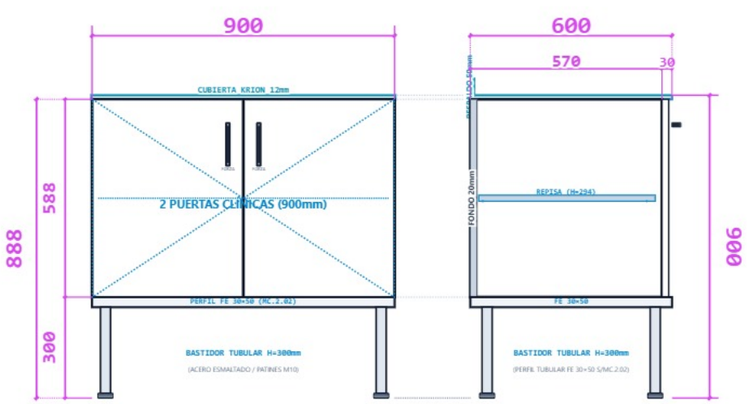


VISTA LATERAL

DESPIECE TÉCNICO Y PERFORACIONES

— Cota Corte — Cota Final (+TC) ◆ Lado Canteado

LATERAL

2 UN 20mm (HPL s/ MDF 18mm)

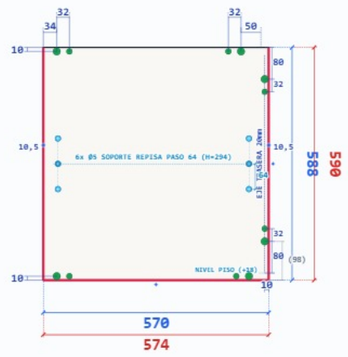


Laterales del gabinete • Canteado Clínico MINSAL

DXF CNC

PISO

1 UN 20mm (HPL s/ MDF 18mm)

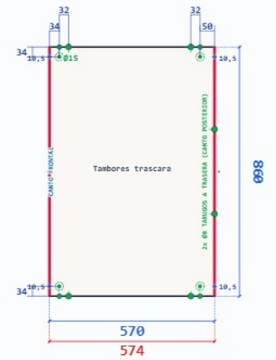


Piso del gabinete con sellado higiénico frontal y posterior (Bastidor metálico MC.2.02) • Canteado Clínico

DXF CNC

TAPA SUPERIOR COMPLETA

1 UN 20mm (HPL s/ MDF 18mm)

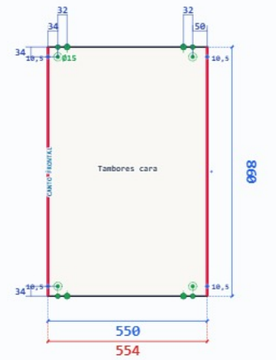


Placa superior completa de melamina para soporte higiénico de cubierta clínica (MC.2.02) • Canteado

DXF CNC

FONDO TRASERA

1 UN 20mm (HPL s/ MDF 18mm)

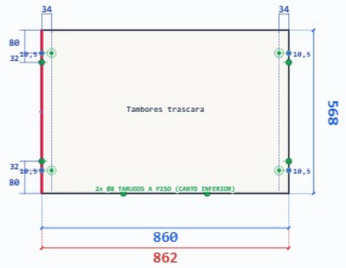


Tapa trasera de melamina/HPL 20mm que parte desde la cara superior del piso hasta la cota superior • Canteado

DXF CNC

REPISA

1 UN 20mm (HPL s/ MDF 18mm)

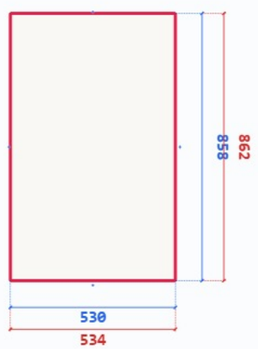


1 repisa(s) interior(es) regulable(s) • Canteado Clínico MINSAL

DXF CNC

PUERTA FRONTAL CLÍNICA (KUTZ)

2 UN 20mm (HPL s/ MDF 18mm)

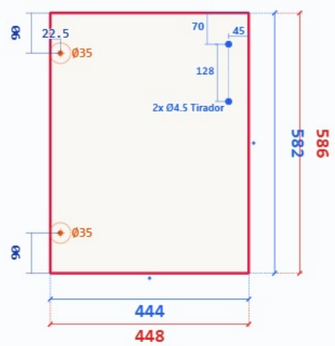

Puertas batientes clínicas de 2 hojas simétricas (holgura ext. 1mm, luz central 2mm | corte 444mm, final 448mm)

DXF CNC

DETALLE 1 **FONDO ESTRUCTURAL**
Melamina 20mm • Placa maciza

DETALLE 2 **ENSAMBLE ESTRUCTURAL**
Minifix 34mm + Tarugo

DETALLE 3 **CAZOLETA BISAGRA**
Eje a 22.5mm • A 90mm ext.

DETALLE 4 **SOPORTE REPISA**
Pernos anti-vuelco

PROYECTO COCINA ARQUIFY

CLIENTE: CLIENTE PARTICULAR
LÁMINA: PLANOS DE FABRICACIÓN: MUEBLE BASE
CONTENIDO: MUEBLE BASE [CASCO S/ BASTIDOR] (900x590x600 mm)

DIBUJANTE: ARQUIFY BIM CAD FECHA: 26/10/2026

OBSERVACIONES CLÍNICAS MC.2.02

- **CAJAS / CASCO:** MDF 18mm laminado blanco 2 caras con TC PVC 22x0.45mm
- **FRENTES:** MDF 18mm laminado blanco 2 caras con TC PVC 22x2.0mm PUR
- **ADHESIVO:** Poliuretano Reactivo (PUR) estanco anti-humedad

Correderas: **Rieles Telescópicos (13mm c/lado)** • Base de cajón: 364mm encajada entre laterales

NOMENCLATURA DE COTAS

- PIEZA FINAL
- MINIFIX / TARUGO
- COTA ARQUITECTÓNICA
- CORTE / EJE
- EJE CANTO (◆)

IDENT. ETIQ. **B-1**


LÁMINA: 03 / 10
ESCALA: S.E (A3)

arquify

ESQUEMA DE CORTE & OPTIMIZACIÓN #1

MATERIAL: **ABET LAMINATI / PROVELCAR BLANCO INTERNI (LAMINADO HPL 2 CARAS)** • FORMATO: **3050 X 1300 X 0.9 MM**

APROVECHAMIENTO
85.8%

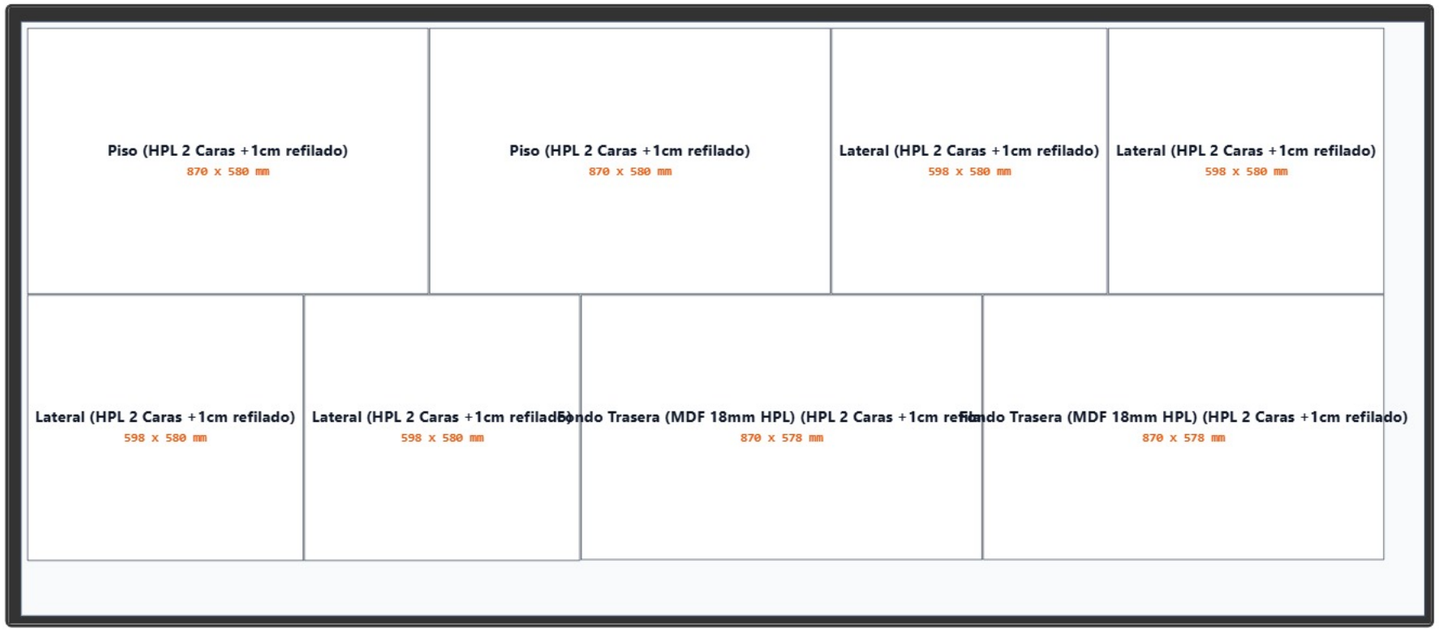

Formato Plancha: 3050 x 1300 mm **Espesor Hoja Sierra:** 3.2 mm **Margen Refilado:** 15 mm **Total Piezas Plancha:** 8 un.

PROYECTO COCINA ARQUIFY

CLIENTE: CLIENTE PARTICULAR
LÁMINA: OPTIMIZACIÓN CORTE: PLANCHA LAMINADO HPL 0.9MM (ABET LAMINATI 2 CARAS) - COLOR: Abet
CONTENIDO: PATRÓN #1 DE 4 (PLANCHA #1) - Abet Laminati / Provelcar Blanco Interni (Laminado HPL 2 Cara

DIBUJANTE: ARQUIFY BIM CAD FECHA: 26/10/2026

PARÁMETROS DE SECCIONADO & CORTE

- **ESPESOR SIERRA (KERF):** 3.2 mm (Disco con incisor)
- **REFILADO PERIMETRAL:** 15 mm mínimo por lado
- **SENTIDO DE VETA:** Longitudinal en frentes y tapas vistas

Algoritmo: **Guillotina 2D CAD/CAM**

CONVENCIONES DE CORTE

PIEZA ÚTIL
RETAZO / MERMA
LÍNEA CORTE
TAPACANTO
DIRECCIÓN VETA ↔ LONGITUDINAL

IDENT. ETIQ.
OPT-1


LÁMINA: 04 / 10
ESCALA: S.E (A3)

arquify

ESQUEMA DE CORTE & OPTIMIZACIÓN #2

MATERIAL: **ABET LAMINATI / PROVELCAR BLANCO INTERNI (LAMINADO HPL 2 CARAS)** • FORMATO: **3050 X 1300 X 0.9 MM**

APROVECHAMIENTO
68.6%

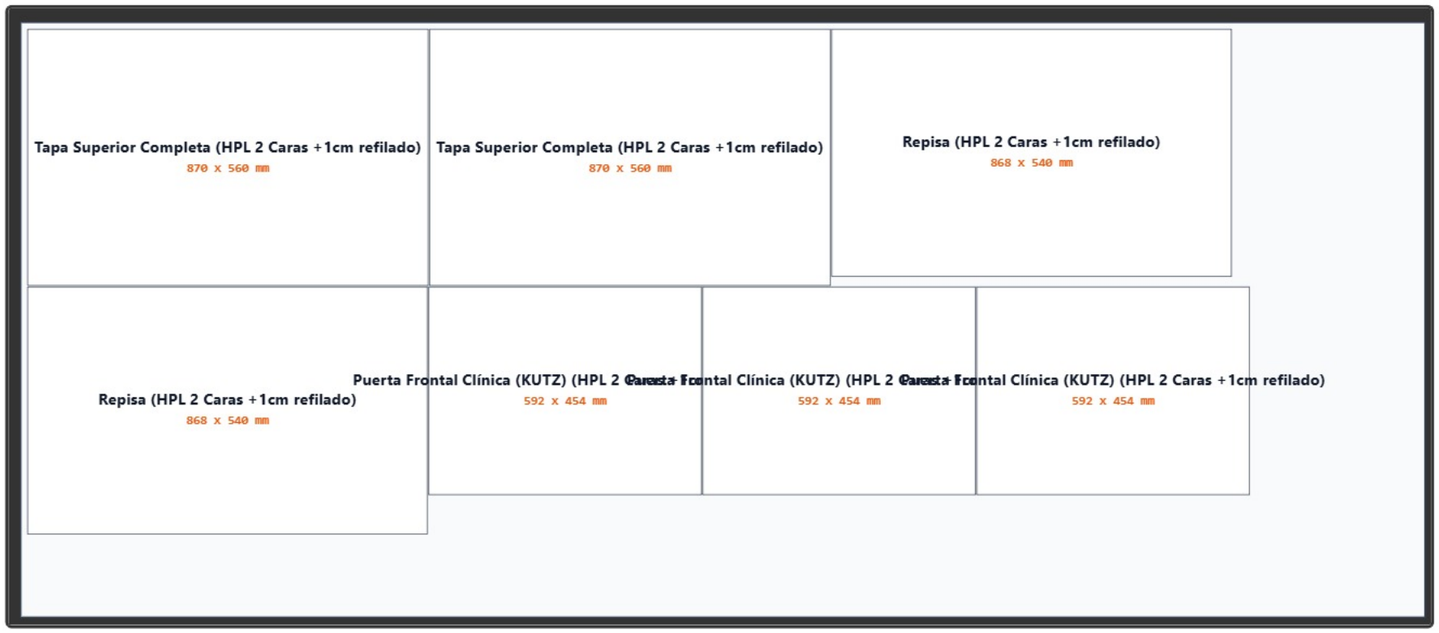

Formato Plancha: 3050 x 1300 mm **Espesor Hoja Sierra:** 3.2 mm **Margen Refilado:** 15 mm **Total Piezas Plancha:** 7 un.

PROYECTO COCINA ARQUIFY

CLIENTE: CLIENTE PARTICULAR
LÁMINA: OPTIMIZACIÓN CORTE: PLANCHA LAMINADO HPL 0.9MM (ABET LAMINATI 2 CARAS) - COLOR: Abet
CONTENIDO: PATRÓN #2 DE 4 (PLANCHA #2) - Abet Laminati / Provelcar Blanco Interni (Laminado HPL 2 Cara

DIBUJANTE: ARQUIFY BIM CAD FECHA: 26/10/2026

PARÁMETROS DE SECCIONADO & CORTE

- **ESPESOR SIERRA (KERF):** 3.2 mm (Disco con incisor)
- **REFILADO PERIMETRAL:** 15 mm mínimo por lado
- **SENTIDO DE VETA:** Longitudinal en frentes y tapas vistas

Algoritmo: **Guillotina 2D CAD/CAM**

CONVENCIONES DE CORTE

- PIEZA ÚTIL
- RETAZO / MERMA
- LÍNEA CORTE
- TAPACANTO

DIRECCIÓN VETA ↔ LONGITUDINAL

IDENT. ETIQ.
OPT-2

LÁMINA: 05 / 10
ESCALA: S.E (A3)

arquify

ESQUEMA DE CORTE & OPTIMIZACIÓN #3

MATERIAL: **ABET LAMINATI / PROVELCAR BLANCO INTERNI (LAMINADO HPL 2 CARAS)** • FORMATO: **3050 X 1300 X 0.9 MM**

APROVECHAMIENTO
6.8%



Formato Plancha: 3050 x 1300 mm **Espesor Hoja Sierra:** 3.2 mm **Margen Refilado:** 15 mm **Total Piezas Plancha:** 1 un.

PROYECTO COCINA ARQUIFY

CLIENTE: CLIENTE PARTICULAR
LÁMINA: OPTIMIZACIÓN CORTE: PLANCHA LAMINADO HPL 0.9MM (ABET LAMINATI 2 CARAS) - COLOR: Abet
CONTENIDO: PATRÓN #3 DE 4 (PLANCHA #3) - Abet Laminati / Provelcar Blanco Interni (Laminado HPL 2 Cara

DIBUJANTE: ARQUIFY BIM CAD FECHA: 26/10/2026

PARÁMETROS DE SECCIONADO & CORTE

- **ESPESOR SIERRA (KERF):** 3.2 mm (Disco con incisor)
- **REFILADO PERIMETRAL:** 15 mm mínimo por lado
- **SENTIDO DE VETA:** Longitudinal en frentes y tapas vistas

Algoritmo: **Guillotina 2D CAD/CAM**

CONVENCIONES DE CORTE

- PIEZA ÚTIL
- LÍNEA CORTE
- RETAZO / MERMA
- TAPACANTO

DIRECCIÓN VETA ↔ LONGITUDINAL

IDENT. ETIQ.
OPT-3

LÁMINA: 06 / 10
ESCALA: S.E (A3)


arquify

PATRÓN #4 DE 4 (1 PLANCHAS TOTALES)

ESQUEMA DE CORTE & OPTIMIZACIÓN #4

MATERIAL: **MDF CRUDO 18MM (SUSTRATO BASE)** • FORMATO: `2440 X 1830 X 18 MM`

APROVECHAMIENTO
69.3%

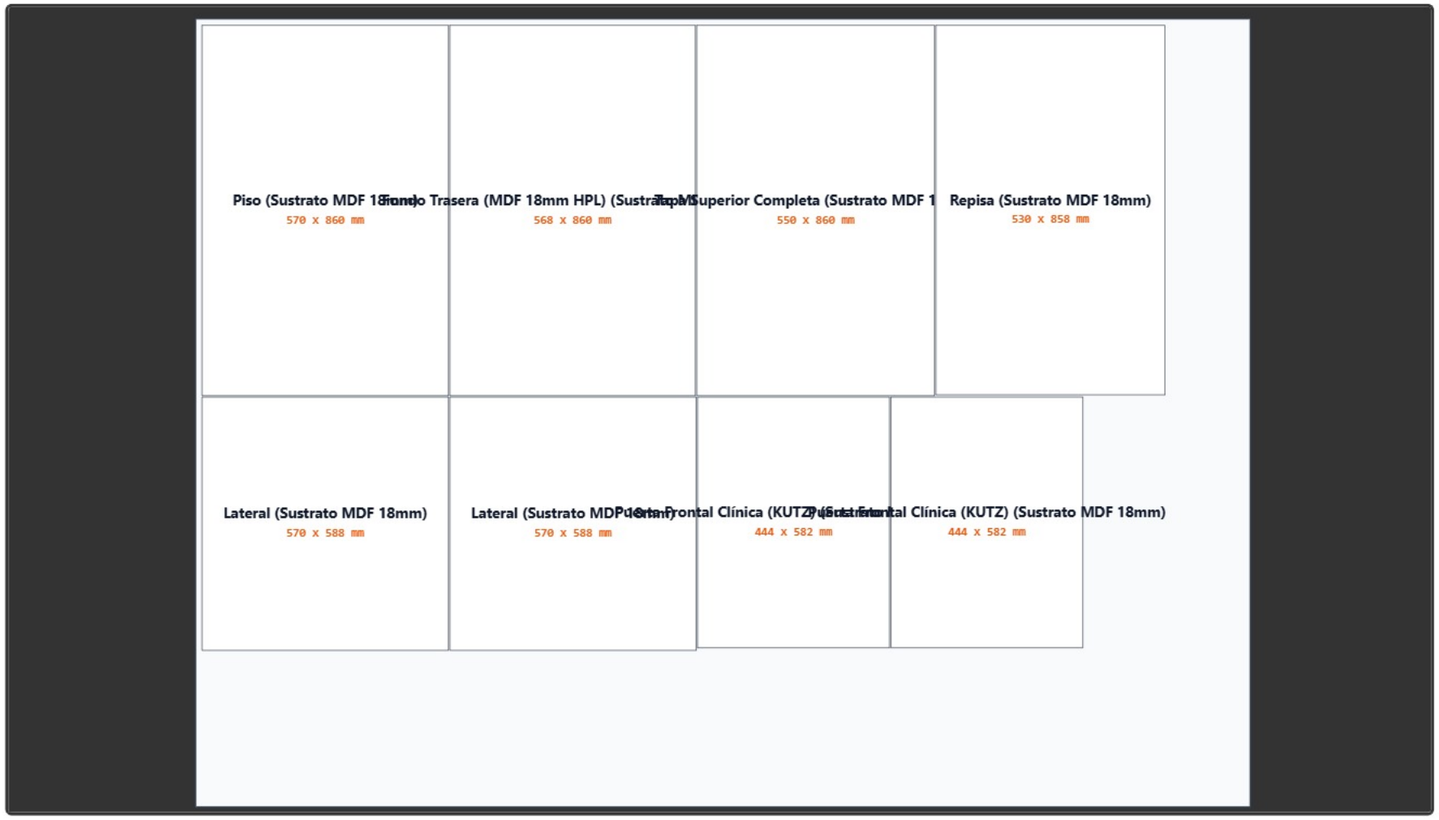

Formato Plancha: 2440 x 1830 mm **Espesor Hoja Sierra:** 3.2 mm **Margen Refilado:** 15 mm **Total Piezas Plancha:** 8 un.

PROYECTO COCINA ARQUIFY

CLIENTE: CLIENTE PARTICULAR
LÁMINA: OPTIMIZACIÓN CORTE: PLANCHA MDF CRUDO 18MM (SUSTRATO ESTRUCTURA, PUERTAS Y CAJONI
CONTENIDO: PATRÓN #4 DE 4 (PLANCHA #4) - MDF Crudo 18mm (Sustrato Base) 18mm

DIBUJANTE: ARQUIFY BIM CAD FECHA: 26/10/2026

PARÁMETROS DE SECCIONADO & CORTE

- **ESPESOR SIERRA (KERF):** 3.2 mm (Disco con incisor)
- **REFILADO PERIMETRAL:** 15 mm mínimo por lado
- **SENTIDO DE VETA:** Longitudinal en frentes y tapas vistas

Algoritmo: **Guillotina 2D CAD/CAM**

CONVENCIONES DE CORTE

- PIEZA ÚTIL
- RETAZO / MERMA
- LÍNEA CORTE
- TAPACANTO

DIRECCIÓN VETA ↔ LONGITUDINAL

IDENT. ETIQ.
OPT-4

LÁMINA: 07 / 10
ESCALA: S.E (A3)

arquify

PATRÓN #1 DE 1 (1 PLANCHAS TOTALES)

ESQUEMA DE CORTE & OPTIMIZACIÓN EN PLANCHA #1

MATERIAL: **KRION SOLID SURFACE BLANCO (1100 SNOW WHITE EAST 12MM)** • ESPESOR: **12 MM** • CRITERIO LOGÍSTICO: **CASA (MÁX 2500 MM)**

APROVECHAMIENTO
22%
Útil: 0.603 m² | Retazo: 2.194 m²



Formato Plancha: 3680 x 760 mm **Espesor Disco Diamante:** Kerf 3.5 mm **Despunte Perimetral:** 10 mm **Criterio Logístico:** Casa (máx 2500 mm)

Cubierta Faldón Respaldo Cascada Encastre

PROYECTO COCINA ARQUIFY

CLIENTE: CLIENTE PARTICULAR
LÁMINA: OPTIMIZACIÓN CUBIERTA KRION SOLID SURFACE BLANCO (1100 SNOW WHITE EAST 12MM): PLANC
CONTENIDO: Krion Solid Surface Blanco (1100 Snow White EAST 12mm)

DIBUJANTE: ARQUIFY BIM CAD FECHA: 26/10/2026

ESPECIFICACIONES DE CUBIERTA SANITARIA

- **MATERIAL:** Krion Solid Surface Snow White / HPL Compacto 12mm
- **TERMINACIÓN:** Canto macizo 12mm pulido sanitario sin filo
- **ASEPSIA:** Superficie no porosa, sin uniones perceptibles

Logística: **Largo máx. continuo 2.50m**

PIEZAS PÉTREAS QSTONE

- CUBIERTA / ISLA
- CASCADA LATERAL
- RETAJO APROVECHABLE
- FALDÓN FRONTAL
- RESPALDO MURO

IDENT. ETIQ.
QS-1

LÁMINA: 08 / 10
ESCALA: S.E (A3)

arquify

LISTADO CONSOLIDADO DE MATERIALES E INSUMOS (BOM)

SISTEMA: MINIFIX + TARUGO 8X30 • CORREDERAS: TELESCOPICA • TABLEROS FORMATO ESTÁNDAR

Ítems 1 - 15 de 18

CATEGORÍA	ÍTEM / COMPONENTE	CANTIDAD	UNIDAD	DETALLES DE APLICACIÓN
[redacted]	Plancha Laminado HPL (Abet Laminati / Provelcar Blanco Interni)	3	Planchas (3050x1300x0.9mm)	Área neta: 6.39 m² | Aprovechamiento est.: 53.7% (Patrón #1 + Patrón #2 + Patrón #3)
[redacted]	Plancha MDF Crudo / Sustrato Base p/ HPL (18mm)	1	Planchas (2440x1830x18mm)	Área neta: 3.09 m² | Aprovechamiento est.: 69.3% (Patrón #4)
[redacted]	Adhesivo de Contacto Alta Resistencia (Prensado HPL)	2	Litros / Galón	Pegado de alta resistencia HPL sobre sustrato MDF 18mm (6.2 m² caras)
[redacted]	Plancha Cubierta Krion Solid Surface Blanco (1100 Snow White EAST 12mm) (12mm)	1	Planchas (3680x760x12mm)	Área neta útil: 0.60 m² | Aprovechamiento est.: 22% (Patrón #1)
[redacted]	Adhesivo Bicomponente Krion® / Solid Surface (Tubo 250ml al tono)	1	Cartuchos	Pegado químico homogéneo sin poros ni juntas visibles (2.4 m lineales pulidos)
[redacted]	Sellador Elastomérico Fungicida Aséptico (Silicona Sanitaria)	1	Cartucho	Sellado perimetral posterior y estanqueidad contra muro
[redacted]	Tapacanto PVC Puertas y Frentes (22x2.00mm)	5	Metros Lineales	Terminación perimetral frentes (Abet Laminati / Provelcar Blanco Interni)
[redacted]	Tapacanto PVC Estructura (22x2.00mm)	12	Metros Lineales	Cantos frontales e interiores de gabinetes (Abet Laminati / Provelcar Blanco Interni)
[redacted]	Pernos Minifix + Cajas Excéntricas 15mm	20	Juegos	Estructura (20) + Cajones (0)
[redacted]	Tarugos de Madera 8x30mm	40	Unidades	Encastre y alineación estructural mecanizada
[redacted]	Tapas Adhesivas Embellecedoras para Minifix (Ø15mm)	20	Unidades	Ocultamiento estético de cajas excéntricas
[redacted]	Bisagras Cazoleta 35mm Rectas (Cierre Suave)	4	Unidades	Puertas exteriores de gabinetes y despensas
[redacted]	Tornillos Fijación Bisagras 3.5x16mm	16	Unidades	Para cazoleta y base de montaje
[redacted]	Soportes de Repisa Niquelados Ø5mm (Pitones con Retén/Goma)	4	Unidades	Montaje y fijación regulable de repisas interiores (1 repisas x 4 soportes)
ESTRUCTURA METÁLICA	Perfil Tubular FE 30x50x1.5mm Esmaltado Blanco (Barra 6m)	1	Barras	Estructura autoportante unificada según Plano Independiente MC.2.02 (1 bancada continua). Total: 3.90 m lineales de perfil tubular.

PROYECTO COCINA ARQUIFY

CLIENTE: CLIENTE PARTICULAR
LÁMINA: LISTADO CONSOLIDADO DE MATERIALES E INSUMOS (BOM) [1/2]
CONTENIDO: CÓMPUTO MÉTRICO, HERRAJES Y FIJACIONES (HOJA 1 DE 2)

DIBUJANTE: ARQUIFY BIM CAD
FECHA: 26/10/2026

CÓMPUTO MÉTRICO & HERRAJES CLÍNICOS

- **BASTIDOR FE:** Perfil tubular FE 30x50x1.5mm esmaltado blanco h=300mm
- **QUINCALLERÍA:** Cerradura Trampa ANVER + Tirador Perfil KUTZ 12/18
- **CORREDERAS:** Ducasse telescópicas A-B + Häfele cierre suave C

Lista Maestra: **Consolidado de Producción**

CONTROL DE FABRICACIÓN

ESTADO: **APROBADO**
REVISIÓN: **REV. A**
TOLERANCIA: **±0.5 mm**
NORMA: **ISO 128**
LISTA VINCULADA AL BOM

IDENT. ETIQ.
BOM-01

LÁMINA: 09 / 10
ESCALA: S.E (A3)

arquify

LISTADO CONSOLIDADO DE MATERIALES E INSUMOS (BOM)

SISTEMA: MINIFIX + TARUGO 8X30 • CORREDERAS: TELESCOPICA • TABLEROS FORMATO ESTÁNDAR

Ítems 16 - 18 de 18

CATEGORÍA	ÍTEM / COMPONENTE	CANTIDAD	UNIDAD	DETALLES DE APLICACIÓN
[redacted]	Patín Regulador Nivelador Metálico Sanitario M10	4	Unidades	Patines reguladores para apoyo y nivelación de estructura tubular independiente (4 puntos de apoyo con base de goma antideslizante lavable).
[redacted]	Tirador / Manilla Tirador Forza (128mm - Negro Mate)	2	Unidades	Fijación frontal/posterior estándar para frentes y puertas
[redacted]	Tornillos M4 x 22mm para Tiradores	4	Unidades	Fijación posterior para frentes de 15/18mm

PROYECTO COCINA ARQUIFY

CLIENTE: CLIENTE PARTICULAR
LÁMINA: LISTADO CONSOLIDADO DE MATERIALES E INSUMOS (BOM) [2/2]
CONTENIDO: CÓMPUTO MÉTRICO, HERRAJES Y FIJACIONES (HOJA 2 DE 2)

DIBUJANTE: ARQUIFY BIM CAD
FECHA: 26/10/2026

CÓMPUTO MÉTRICO & HERRAJES CLÍNICOS

- **BASTIDOR FE:** Perfil tubular FE 30x50x1.5mm esmaltado blanco h=300mm
- **QUINCALLERÍA:** Cerradura Trampa ANVER + Tirador Perfil KUTZ 12/18
- **CORREDERAS:** Ducasse telescópicas A-B + Häfele cierre suave C

Lista Maestra: **Consolidado de Producción**

CONTROL DE FABRICACIÓN

ESTADO: **APROBADO**
REVISIÓN: **REV. A**
TOLERANCIA: **±0.5 mm**
NORMA: **ISO 128**
LISTA VINCULADA AL BOM

IDENT. ETIQ.
BOM-02

LÁMINA: 10 / 10
ESCALA: S.E (A3)

arquify